



A COMMUNITY OF CHOICE

Planning and Development Department

2101 O'Neil Avenue, Suite 202, Cheyenne WY 82001
(Phone) 307-637-6282 (Fax) 307-637-6366

MEMO

To: Honorable Mayor Patrick Collins and Members of the City Council
From: Connor White, Planner II
Subject: County Pocket Annexation #5
Date: May 27, 2025

Background:

The item for consideration is an Ordinance. Annexation of County pockets is a 2022 City Council priority. A "County pocket" is an area of unincorporated land 100% surrounded by the City of Cheyenne. A related "Assigned Zoning" pursuant to Unified Development Code (UDC) Section 2.2.8 ordinance is also on the agenda.

The proposed Governing Body review schedule is as follows:

- Introduction and referral: May 27, 2025
- Public Services Committee: June 2, 2025
- Second Reading: June 9, 2025
- Public Services Committee: June 16, 2025
- Third and Final Reading: June 23, 2025

This annexation is comprised of 95 properties 100% surrounded by the City (See attached map). Of the 95 parcels, a majority are developed with residential uses, several are developed with commercial uses and others are undeveloped or incorporated into adjacent parcels under similar ownership. The City has maintained contact with the County Planning Office to coordinate any pending permits or development reviews. Currently there are no active permits or development specific to the properties proposed for annexation.

On April 1, 2025, City staff mailed a courtesy notice by first class mail to all landowners included in this annexation area inviting them to a "Question and Answer" on Tuesday April 15, 2025. Discussion, comments, and questions primarily surrounded the annexation component and trash collection. During the meeting staff provided information regarding trash collection, snow plowing, water and sewer services and what to expect with the annexation.

The existing use of any property annexed, including any livestock use, will be allowed to continue as is as a nonconforming use. Nonconforming uses may continue until they are abandoned for a period of 12-months. Residents within pockets have been encouraged to complete a Land Use Documentation form detailing the existing use of the land for documentation purposes. At the time of drafting of this memo, four property owners within the area has completed a land use documentation form.

Providing a completed form is not required nor does it prohibit a property owner from making future claims that a use was pre-existing. The form is simply a tool to assist future City staff members to determine if a use was in existence at the time of annexation.

City-initiated annexations do not require an owner's signature. To initiate an annexation, the City must adopt a resolution certifying that the annexation complies with Wyoming State Statute § 15-1-402. After the City adopts this resolution, the annexation follows the typical schedule, including a public hearing and the approval of an Ordinance which annexes the land. The Governing Body adopted Resolution No. 6464 initiating this annexation on May 12, 2025.

As with any annexation, City services will be extended to service the land contained in the annexation. City utilities are already located in the vicinity. Police, fire, and sanitation services will be provided. As several parcels of land contained in this annexation area are developed, City sanitation service will need to be established and landowners have been notified of this required change. Infrastructure improvements required related to the annexation are minimal. Future development such as subdivision or new development will require on- and off-site infrastructure improvements. Existing infrastructure will remain as is upon annexation.

The areas proposed for annexation are adjacent to land under City jurisdiction. Development in this area is a natural extension of the City. 100 % of the perimeter of the annexation area is contiguous to City limits.

Due to meeting the review criteria found in Wyoming Statute § 15-1-402 and the annexation conforming with the 2022 City Council goal to annex County pockets, staff recommends approval of this annexation.

Staff Recommendation:

Staff recommends the Governing Body approve the Annexation Ordinance.

Attachments:

1. Proposed Ordinance (includes Annexation Map as Attachment A)
2. Staff Report

ORDINANCE NO. _____

ENTITLED: “AN ORDINANCE ANNEXING TO THE CITY OF CHEYENNE, WYOMING, VARIOUS TRACTS OF LAND COMPLETELY SURROUNDED BY CURRENT CITY LIMITS SITUATE IN NORTHEAST CHEYENNE GENERALLY LOCATED NORTH OF DELL RANGE BOULEVARD, EAST AND WEST OF RIDGE ROAD AND SOUTH OF STOREY BOULEVARD.”

BE IT ORDAINED BY THE GOVERNING BODY OF THE CITY OF CHEYENNE, WYOMING:

Section 1. That the City of Cheyenne hereby finds as follows:

(a) That the City of Cheyenne has initiated this annexation in compliance with Wyo. Stat. § 15-1-404, and adopted on May 12, 2025, Resolution No. 6464 certifying that the area to be annexed complies with the requirements of Wyo. Stat. § 15-1-402;

(b) That an accurate legal description of said land is as follows:

Various tracts of land situate in northeast Cheyenne, more particularly described as follows:

Area A:

TRACTS 1 THRU 8, 30 FEET OF VACATED GROVE AVENUE, TRACT 13 EXCEPT THE WEST 36 FEET, TRACTS 14, 15 AND 16, BLOCK 1 AND THE 16' ALLEY ADJACENT THERETO, HOLLAND SMITH SUBDIVISION, CITY OF CHEYENNE, LARAMIE COUNTY, WYOMING.

SAID AREA CONTAINS 2.66 ACRES MORE OR LESS.

Area B:

THE WEST 435 FEET OF THE SOUTH 1/2 OF TRACT 31, DELL RANGE ADDITION, 2ND FILING, CITY OF CHEYENNE, LARAMIE COUNTY, WYOMING.

SAID AREA CONTAINS 2.94 ACRES MORE OR LESS.

Area C:

THE NORTH 192.18 FEET OF THE SOUTH 256.24 FEET OF THE WEST 340 FEET OF TRACT 4, DELL RANGE ADDITION, PLUS (RES

961104-02, B00K 1438, PAGE 1138, 6665.4 SQ') VACATED SUNRISE HILLS DRIVE, LOTS 2, 3, 6 AND 7, BLOCK 5; SUN RISE HILLS ADDITION - FILING NO. 1, PLUS (5100 SQ', RES #961104-02) VACATED SUNRISE HILLS DRIVE, CITY OF CHEYENNE, LARAMIE COUNTY, WYOMING.

SAID AREA CONTAINS 1.65 ACRES MORE OR LESS.

Area D:

THE NORTH 140.52 FEET OF THE SOUTH 281.04 FEET OF THE WEST 310 FEET OF TRACT 5 AND THE WEST 200 FEET OF THE NORTH 110.52 FEET OF THE SOUTH 140.52 FEET OF THE WEST 213.84 FEET OF TRACT 5, DELL RANGE ADDITION, CITY OF CHEYENNE, LARAMIE COUNTY, WYOMING.

SAID AREA CONTAINS 1.65 ACRES MORE OR LESS.

Area E:

LOT 6, 7, 8, 9 AND 12, DELL RANGE ADDITION, REPLAT OF THE SOUTH 1/2 OF TRACT 13, CITY OF CHEYENNE, LARAMIE COUNTY, WYOMING.

SAID AREA CONTAINS 0.84 ACRES MORE OR LESS.

Area F:

ALL THAT PORTION OF TRACT 20, DELL RANGE ADDITION, BEING A SUBDIVISION OF THE WEST HALF OF SECTION 22, TOWNSHIP 14 NORTH, RANGE 66 WEST OF THE 6TH P.M., LARAMIE COUNTY, WYOMING, DESCRIBED AS FOLLOWS:

BEGINNING AT A POINT OF THE EAST BOUNDARY OF A PARCEL OF LAND DESCRIBED IN THAT CERTAIN DEED RECORDED IN BOOK 1061 AT PAGE 297 OF THE LARAMIE COUNTY RECORDS WHICH POINT BEARS S.0°32.5'E. A DISTANCE OF 105.0 FEET FROM A POINT ON THE NORTH BOUNDARY OF SAID TRACT 20 FROM WHICH THE NORTHEAST CORNER THEREOF BEARS EAST A DISTANCE OF 123.4 FEET (124 FEET IN BOOK 1061 AT PAGE THENCE S. 0°32.5 E. ALONG SAID EAST BOUNDARY A DISTANCE OF 45.0 FEET TO THE SOUTHEAST CORNER OF SAID PARCEL OF LAND MARKED BY REBAR WITH AN ALUMINUM I.D. CAP ATTACHED; THENCE S. 89°59'W. ALONG THE SOUTH BOUNDARY OF SAID PARCEL OF LAND A DISTANCE OF 124.5 FEET (124 FEET IN BOOK 1061 AT PAGE 297) TO A POINT MARKED BY A REBAR

WITH AN ALUMINUM I.D. CAP ATTACHED; THENCE N 0°30'W. ALONG THE WEST BOUNDARY OF SAID PARCEL OF LAND A DISTANCE OF 45.0 FEET TO A POINT MARKED BY A NO.5 REBAR WITH AN ALUMINUM I.D. CAP ATTACHED; THENCE N 89°59'E. A DISTANCE OF 124.5 FEET TO THE POINT OF BEGINNING.

SAID AREA CONTAINS 0.15 ACRES MORE OR LESS.

Area G:

LOT 5, COLE HEIGHTS ADDITION AND THE ADJACENT 60' RIGHT OF WAY OF COLE PLACE, CITY OF CHEYENNE, LARAMIE COUNTY, WYOMING.

SAID AREA CONTAINS 0.50 ACRES MORE OR LESS.

Area H:

ALL PARCELS AND PLATTED RIGHTS OF WAY LOCATED WITHIN: BEGINNING AT THE SOUTHWEST CORNER OF LOT 5, BLOCK 4, GOULD SUBDIVISION, THENCE SOUTHERLY ALONG THE EASTERLY RIGHT OF WAY OF CINDY AVE. A DISTANCE OF 195.00 FEET TO A POINT ON THE SOUTHERLY RIGHT OF WAY OF EVERTON DR.; THENCE WESTERLY ALONG SAID RIGHT OF WAY 30.00 FEET TO THE NORTHEASTERLY CORNER OF TRACT 20 OF GREEN SUBDIVISION OF THE NORTH HALF OF TRACT 19, DELL RANGE ADDITION; THENCE SOUTHERLY A DISTANCE OF 600.00 FEET ALONG THE EASTERLY BOUNDARIES OF GREEN SUBDIVISIONS OF BOTH THE NORTH HALF AND SOUTH HALF OF TRACT 19, DELL RANGE ADDITION TO A POINT ON THE NORTHERLY RIGHT OF WAY OF GREGG WAY; THENCE WESTERLY ALONG SAID RIGHT OF WAY A DISTANCE OF 700.60 FEET TO THE SOUTHEASTERLY CORNER OF TRACT 20, DELL RANGE ADDITION; THENCE INCLUSIVE OF EXISTING PARCELS BEING PORTIONS OF TRACT 20, DELL RANGE ADDITION DESCRIBED AS CONTINUING WESTERLY ALONG SAID RIGHT OF WAY A DISTANCE OF 108 FEET TO A POINT; THENCE NORTHERLY 140.00 FEET TO A POINT; THENCE WESTERLY 140.00 FEET TO A POINT ON THE EASTERLY RIGHT OF WAY OF VOSLER PLACE; THENCE NORTHERLY ALONG SAID RIGHT OF WAY 175.00 FEET TO THE SOUTHWESTERLY CORNER OF LOT 1, BLOCK 1, CROW ADDITION; THENCE ALONG THE BOUNDARY OF SAID CROW ADDITION THE FOLLOWING FOUR COURSES; THENCE EASTERLY A DISTANCE OF 124.00 FEET TO A POINT; THENCE NORTHERLY 100 FEET TO A POINT; THENCE EASTERLY 124.00 FEET TO A POINT ON THE WESTERLY RIGHT OF WAY OF

RIDGE ROAD; THENCE NORTHERLY ALONG SAID RIGHT OF WAY A DISTANCE OF 195.00 FEET TO THE POINT OF INTERSECTION WITH THE SOUTHERLY RIGHT OF WAY OF BASIN STREET EXTENDED; THENCE EASTERLY 80.00 FEET TO A POINT ON THE EASTERLY RIGHT OF WAY OF RIDGE ROAD; THENCE NORTHERLY ALONG SAID RIGHT OF WAY, BEING THE WESTERLY BOUNDARY OF GOULD SUBDIVISION, A DISTANCE OF 650 FEET TO THE NORTHWESTERLY CORNER OF LOT 5, BLOCK 2, GOULD SUBDIVISION; THENCE EASTERLY ALONG THE SOUTHERLY RIGHT OF WAY OF CARLA DRIVE A DISTANCE OF 1483.80 FEET TO THE NORTHEASTERLY CORNER OF LOT 5, BLOCK 1, SEAVER SUBDIVISION; THENCE THE FOLLOWING THREE COURSES ALONG THE BOUNDARIES OF SEILOFF ADDITION, THENCE SOUTHERLY 180.02 FEET; THENCE EASTERLY 68.00 FEET; THENCE NORTHERLY 180.02 FEET TO THE SOUTHERLY RIGHT OF WAY OF CARLA DRIVE; THENCE CONTINUING EASTERLY ALONG SAID SOUTHERLY RIGHT OF WAY A DISTANCE OF 315.40 FEET TO THE NORTHEASTERLY CORNER OF LOT 1, BLOCK 1, SEAVERS SUBDIVISION; THENCE SOUTHERLY ALONG THE WESTERLY RIGHT OF WAY OF COLLEGE DRIVE A DISTANCE OF 600.00 FEET TO THE SOUTHEASTERLY CORNER OF LOT 2, BLOCK 2, SEAVERS SUBDIVISION; THENCE WESTERLY 389.00 FEET ALONG THE NORTHERLY RIGHT OF WAY OF EVERTON DRIVE TO THE SOUTHWESTERLY CORNER OF LOT 3, BLOCK 2, SEAVERS SUBDIVISION; THENCE NORTHERLY 330.00 FEET TO THE SOUTHEASTERLY CORNER OF DONOVAN SUBDIVISION; THENCE WESTERLY A DISTANCE OF 233.80 FEET ALONG THE NORTHERLY RIGHT OF WAY OF VICTORIA DRIVE TO THE SOUTHEASTERLY CORNER OF LOT 2, BLOCK 1, GOULD SUBDIVISION 2ND FILING; THENCE SOUTHERLY A DISTANCE OF 195.00 FEET TO THE SOUTHEASTERLY CORNER OF LOT 1, BLOCK 4, GOULD SUBDIVISION; THENCE WESTERLY A DISTANCE OF 120.00 FEET TO THE SOUTHWESTERLY CORNER OF SAID LOT 1, BLOCK 4, GOULD SUBDIVISION; THENCE SOUTHERLY A DISTANCE OF 135.00 FEET TO THE SOUTHEASTERLY CORNER OF LOT 9, BLOCK 4, GOULD SUBDIVISION; THENCE WESTERLY A DISTANCE OF 120.00 FEET ALONG THE NORTHERLY RIGHT OF WAY OF EVERTON DRIVE TO THE SOUTHWESTERLY CORNER OF SAID LOT 9; THENCE NORTHERLY A DISTANCE OF 135.00 FEET TO THE NORTHWESTERLY CORNER OF SAID LOT 9; THENCE WESTERLY A DISTANCE OF 360.00 FEET TO THE POINT OF BEGINNING.

SAID AREA CONTAINS 34.17 ACRES MORE OR LESS.

- (c) That the annexation of said areas is for the protection of health, safety, and welfare of the persons residing in the areas and the City of Cheyenne;
- (d) That the urban development of the areas sought to be annexed will constitute a natural, geographical, economical and social part of the City of Cheyenne;
- (e) That the areas are a logical and feasible addition to the City and that the extension of basic services such as water and sewer systems, police and fire protection, and other services customarily available in the City of Cheyenne can, within reason, be furnished;
- (f) That the areas are considered contiguous to the City of Cheyenne according to the provisions of Wyo. Stat. § 15-1-402 (b) and is currently zoned A-1 Agricultural and Rural Residential, MR Medium-density Residential, MU Mixed-use and PUD Planned Unit Development by the Laramie County Commissioners; and
- (g) That the City of Cheyenne does not own or operate its own electrical utility, and its governing body is prepared to designate a utility to serve the annexed areas pursuant to Wyo. Stat. § 15-1-410, and to authorize the designated utility to serve the entirety of the annexed areas.

Section 2. That all of the real property described in Section 1(b) of this Ordinance is hereby annexed to the City of Cheyenne, Wyoming, and shall become a part thereof.

Section 3. That pursuant to Wyo. Stat. § 15-1-405, the Governing Body held a public hearing on May 27, 2025, on the proposed annexation and found that the annexation complied Wyo. Stat. § 15-1-402.

Section 4. That the map of the areas to be annexed is shown in Exhibit A, which is attached hereto and incorporated herein, satisfies the requirements of Wyo. Stat. § 15-1-406, and shall be recorded with the Laramie County Clerk in conjunction with this ordinance.

Section 5. That the City Clerk is directed to file an executed copy of this annexation ordinance with the County Clerk and Ex-Officio Register of Deeds for Laramie County, Wyoming, and shall also notify the City Engineer's Office to add said area to the official City Map of the City of Cheyenne, Wyoming.

Section 6. Sections, paragraphs, sentences, clauses and phrases of this ordinance are severable. If any phrase, clause, sentence, paragraph or section of this ordinance is declared illegal or unconstitutional, such illegality or unconstitutionality shall not affect any of the remaining phrases, clauses, sentences, paragraphs and sections.

Section 7. That this ordinance shall be in full force and effect upon its publication.

FIRST READING: _____

SECOND READING: _____

THIRD AND FINAL READING: _____

PATRICK COLLINS, MAYOR

(SEAL)

ATTEST:

KYLIE SODEN, CITY CLERK

Published: _____
Wyoming Tribune-Eagle

ANNEXATION MAP
COUNTY POCKETS
FORCED ANNEXATION #5

SHEET #
1 OF 9



COUNTY POCKETS
FORCED ANNEXATION
NUMBER 5

REVISED: 4/11/2025
25112 VMAP.DWG

STELL SURVEYING SERVICES, LLC
PROFESSIONAL LAND SURVEYORS
PLANNING & DEVELOPMENT SPECIALISTS
1108 WEST 19th ST. CHEYENNE, WY. 82001 • (307) 634-7273
256 GILCHRIST ST. WHEATLAND, WY. 82201 • (307) 582-9789
www.StellSurvey.com • info@StellSurvey.com



BASIS OF BEARINGS:
WYOMING STATE PLANE COORDINATES,
EAST ZONE, NAD83-2011,
US SURVEY FEET, DISTANCES ARE GRID
DISTANCES.

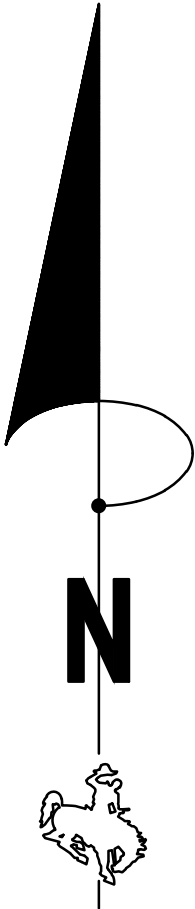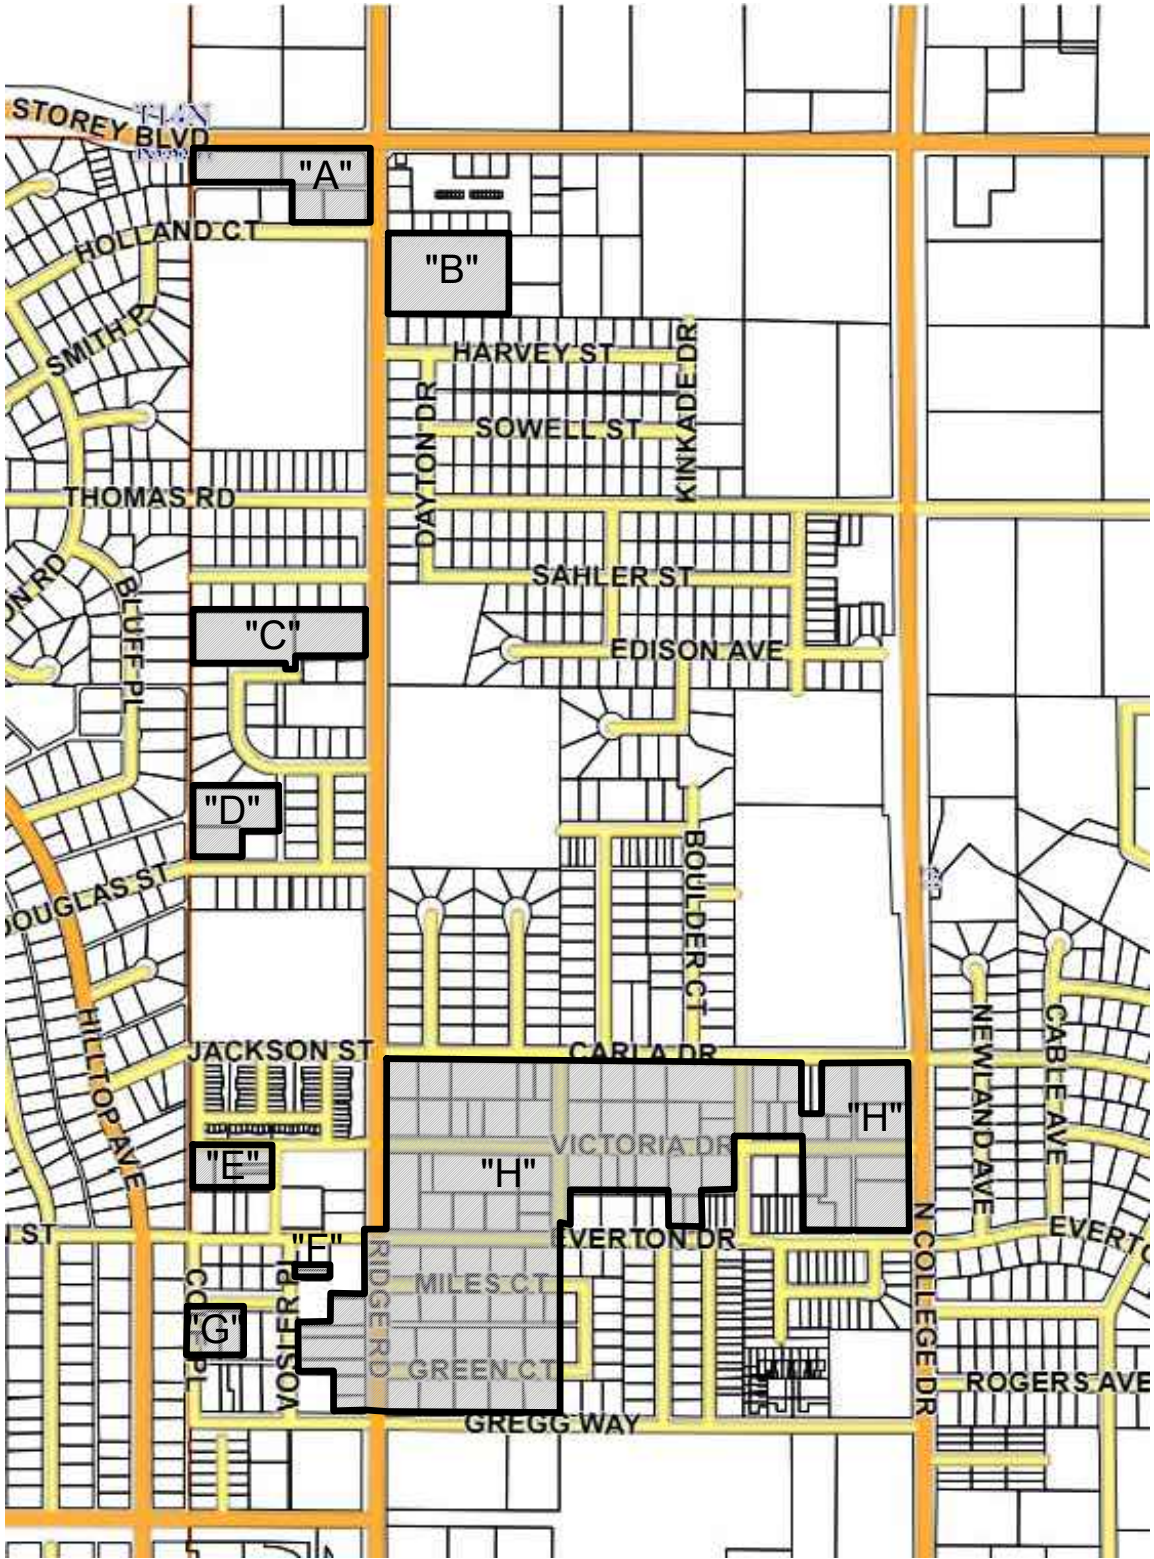

FILING RECORD

VICINITY MAP
(NOT TO SCALE)

PREPARED APRIL 2025

CERTIFICATE OF SURVEYOR

I, JEFFREY B. JONES, A PROFESSIONAL LAND SURVEYOR IN THE STATE OF WYOMING, HEREBY STATE THAT THESE ANNEXATION MAPS WERE PREPARED FROM OFFICIAL PLATS AND DEEDS OF RECORD AND FROM NOTES OF A SURVEY CONDUCTED BY MYSELF OR UNDER MY DIRECT SUPERVISION DURING THE MONTHS OF FEBRUARY –JUNE, 2025, AND THAT THIS MAP CORRECTLY REPRESENTS SAID SURVEY OF THE LAND DEPICTED HEREON TO THE BEST OF MY KNOWLEDGE.

CERTIFICATE OF SURVEYOR

I, JEFFREY B. JONES, A PROFESSIONAL LAND SURVEYOR IN THE STATE OF WYOMING, HEREBY STATE THAT THESE ANNEXATION MAPS WERE PREPARED FROM OFFICIAL PLATS AND DEEDS OF RECORD AND FROM NOTES OF A SURVEY CONDUCTED BY MYSELF OR UNDER MY DIRECT SUPERVISION DURING THE MONTHS OF FEBRUARY-JUNE, 2025, AND THAT THIS MAP CORRECTLY REPRESENTS SAID SURVEY OF THE LAND DEPICTED HEREON TO THE BEST OF MY KNOWLEDGE.

ANNEXATION DESCRIPTION - A

Tracts 1 thru 8, 30 feet of vacated Grove Avenue, Tract 13 except the west 36 feet, Tracts 14, 15 and 16, Block 1 and the 16' alley adjacent thereto, Holland Smith Subdivision, City of Cheyenne, Laramie County, Wyoming.

COUNTY POCKETS
FORCED ANNEXATION
NUMBER 5
EXHIBIT A

REVISED: 5/1/2025
25112 EXHIBIT A.DWG

STEL SURVEYING SERVICES, LLC
PROFESSIONAL LAND SURVEYORS
PLANNING & DEVELOPMENT SPECIALISTS
1108 WEST 10th ST. CHEYENNE, WY. 82001 • (307) 634-7223
256 GILCHRIST ST. WHEATLAND, WY. 82201 • (307) 522-9729
www.StelSurvey.com • info@StelSurvey.com



STOREY BLVD. (90' R/W)

RIDGE ROAD (80' R/W)

HOLLAND CT. (60' R/W)

ANNEXATION AREA

TOTAL AREA: 2.66 ACRES

ABUTTING ANNEXATION AND RATIO TO TOTAL PERIMETER - 100%

LEGEND

- AREA TO BE ANNEXED
- EXISTING CITY LIMITS

FILING RECORD


APPROVALS

Approved by the City Council of the City of Cheyenne, Wyoming, this _____ day of _____, 2025.

Mayor

ATTEST:

City Clerk

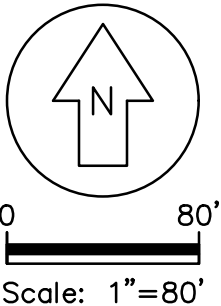

PIDN: AS OF 4-6-25
14662220201500
14662220200700
14662220201100
14662220200600


HOLLAND-SMITH
SUB.

HOLLAND CT.
(60' R/W)

DELL RANGE
ADD
PORTION
T25

RIDGE ROAD (80' R/W)

SUMMIT PARK

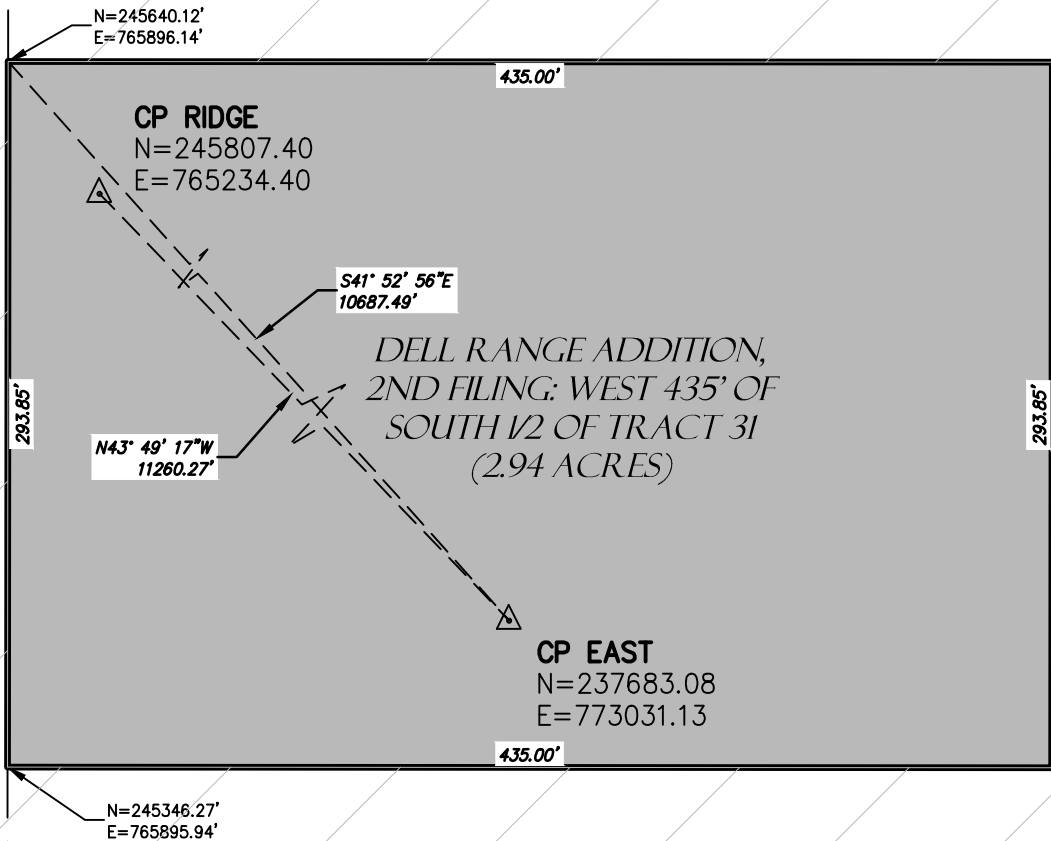

THOMAS HEIGHTS

LEGEND



AREA TO BE ANNEXED



EXISTING CITY LIMITS

ANNEXATION AREA

TOTAL AREA: 2.94 ACRES

ABUTTING ANNEXATION AND RATIO TO TOTAL
PERIMETER - 100%

FILING RECORD

APPROVALS

Approved by the City Council of the City of Cheyenne, Wyoming,
this _____ day of _____, 2025.

Mayor

ATTEST:

City Clerk


CERTIFICATE OF SURVEYOR

I, JEFFREY B. JONES, A PROFESSIONAL LAND SURVEYOR IN THE STATE OF WYOMING, HEREBY STATE THAT THESE ANNEXATION MAPS WERE PREPARED FROM OFFICIAL PLATS AND DEEDS OF RECORD AND FROM NOTES OF A SURVEY CONDUCTED BY MYSELF OR UNDER MY DIRECT SUPERVISION DURING THE MONTHS OF FEBRUARY -JUNE, 2025, AND THAT THIS MAP CORRECTLY REPRESENTS SAID SURVEY OF THE LAND DEPICTED HEREON TO THE BEST OF MY KNOWLEDGE.

ANNEXATION DESCRIPTION - B

THE WEST 435 FEET OF THE SOUTH 1/2 OF TRACT 31,
DELL RANGE ADDITION, 2ND FILING, CITY OF CHEYENNE,
LARAMIE COUNTY, WYOMING.

BASIS OF BEARINGS:
WYOMING STATE PLANE COORDINATES,
EAST ZONE, NAD83-2011,
US SURVEY FEET, DISTANCES ARE GRID
DISTANCES.

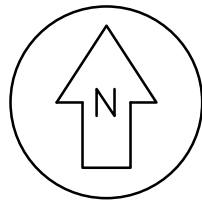

Scale: 1"=80'


SHEET #
3 OF 9

COUNTY POCKETS
FORCED ANNEXATION
NUMBER 5 - EXHIBIT B

REVISED: 4/8/2025
25112 EXHIBIT B.DWG

STELL SURVEYING SERVICES, LLC
PROFESSIONAL LAND SURVEYORS
PLANNING & DEVELOPMENT SPECIALISTS
1108 WEST 10th ST. CHEYENNE, WY. 82001 • (307) 634-7223
256 GILCHRIST ST. WHEATLAND, WY. 82201 • (307) 522-9729
www.StellSurvey.com • info@StellSurvey.com



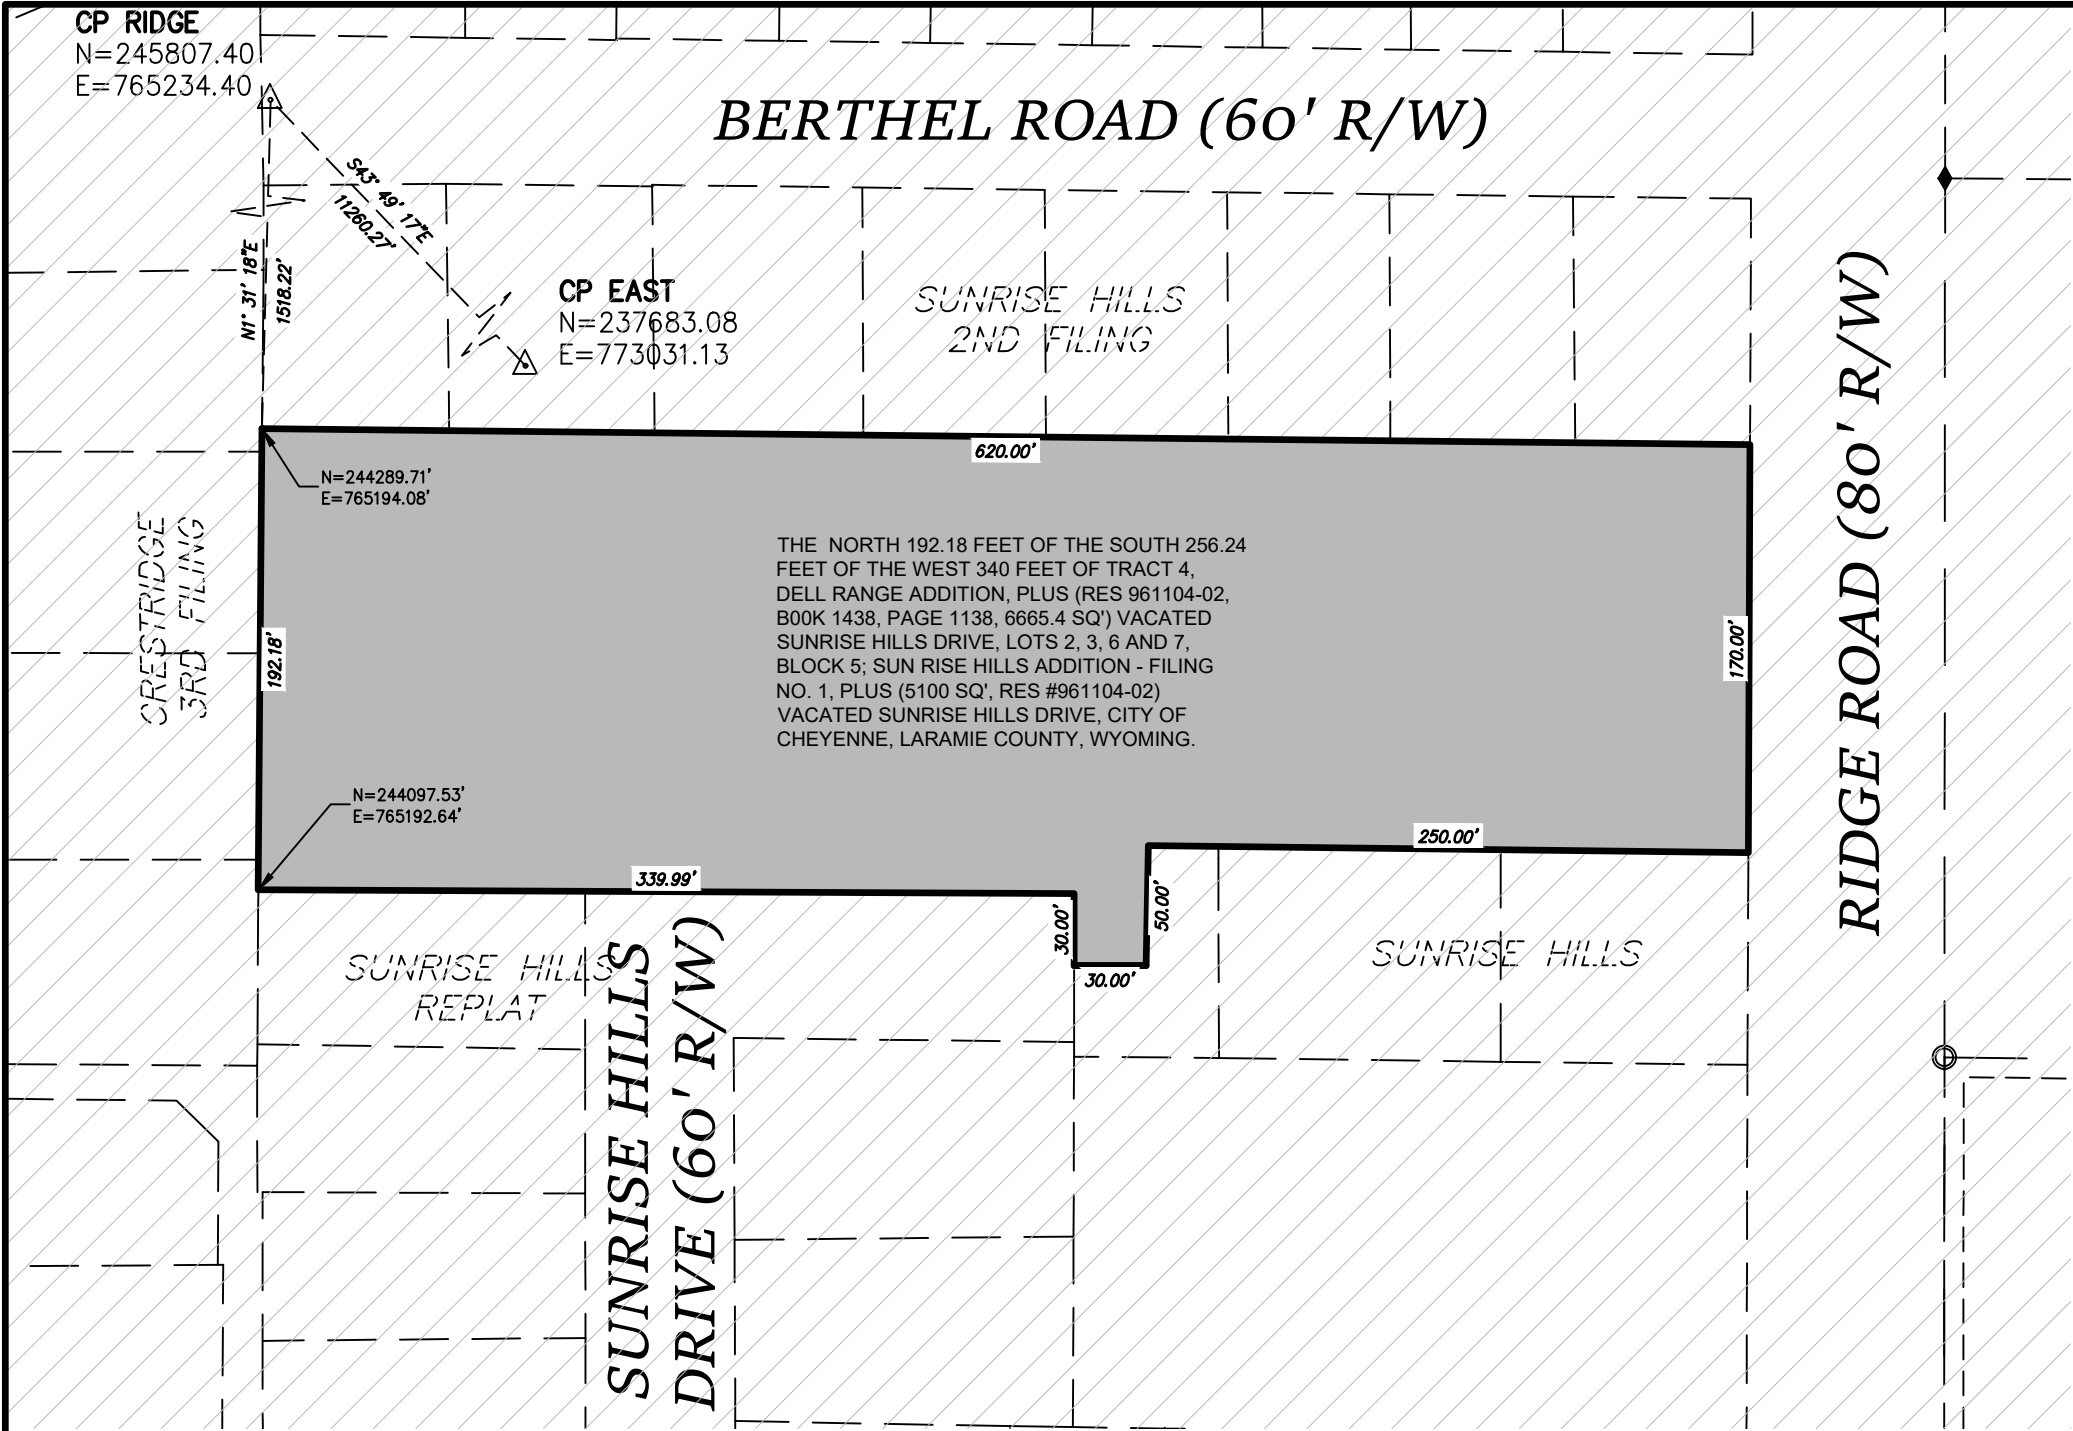

LEGEND



AREA TO BE ANNEXED



EXISTING CITY LIMITS

ANNEXATION AREA

TOTAL AREA: 1.65 ACRES

ABUTTING ANNEXATION AND RATIO TO TOTAL PERIMETER - 100%

APPROVALS

Approved by the City Council of the City of Cheyenne, Wyoming, this _____ day of _____, 2025.

Mayor

ATTEST: _____
City Clerk

FILING RECORD


CERTIFICATE OF SURVEYOR

I, JEFFREY B. JONES, A PROFESSIONAL LAND SURVEYOR IN THE STATE OF WYOMING, HEREBY STATE THAT THESE ANNEXATION MAPS WERE PREPARED FROM OFFICIAL PLATS AND DEEDS OF RECORD AND FROM NOTES OF A SURVEY CONDUCTED BY MYSELF OR UNDER MY DIRECT SUPERVISION DURING THE MONTHS OF FEBRUARY –JUNE, 2025, AND THAT THIS MAP CORRECTLY REPRESENTS SAID SURVEY OF THE LAND DEPICTED HEREON TO THE BEST OF MY KNOWLEDGE.

ANNEXATION DESCRIPTION - C

THE NORTH 192.18 FEET OF THE SOUTH 256.24 FEET OF THE WEST 340 FEET OF TRACT 4, DELL RANGE ADDITION, PLUS (RES 961104-02, B00K 1438, PAGE 1138, 6665.4 SQ') VACATED SUNRISE HILLS DRIVE, LOTS 2, 3, 6 AND 7, BLOCK 5; SUN RISE HILLS ADDITION - FILING NO. 1, PLUS (5100 SQ', RES #961104-02) VACATED SUNRISE HILLS DRIVE, CITY OF CHEYENNE, LARAMIE COUNTY, WYOMING.

BASIS OF BEARINGS:
WYOMING STATE PLANE COORDINATES,
EAST ZONE, NAD83–2011,
US SURVEY FEET, DISTANCES ARE GRID
DISTANCES.

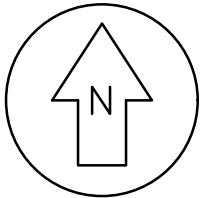

0 80'
Scale: 1"=80'



CERTIFICATE OF SURVEYOR

I, JEFFREY B. JONES, A PROFESSIONAL LAND SURVEYOR IN THE STATE OF WYOMING, HEREBY STATE THAT THESE ANNEXATION MAPS WERE PREPARED FROM OFFICIAL PLATS AND DEEDS OF RECORD AND FROM NOTES OF A SURVEY CONDUCTED BY MYSELF OR UNDER MY DIRECT SUPERVISION DURING THE MONTHS OF FEBRUARY –JUNE, 2025, AND THAT THIS MAP CORRECTLY REPRESENTS SAID SURVEY OF THE LAND DEPICTED HEREON TO THE BEST OF MY KNOWLEDGE.

ANNEXATION DESCRIPTION - D

THE NORTH 140.52 FEET OF THE SOUTH 281.04 FEET OF THE WEST 310 FEET OF TRACT 5 and THE WEST 200 FEET OF THE SOUTH 140.52 FEET OF THE WEST 310 FEET OF TRACT 5, DELL RANGE ADDITION, CITY OF CHEYENNE, LARAMIE COUNTY, WYOMING.

COUNTY POCKETS
FORCED ANNEXATION
NUMBER 5 – EXHIBIT D

REVISED: 5/1/2025
25112 EXHIBIT D.DWG

STIEL SURVEYING SERVICES, LLC
PROFESSIONAL LAND SURVEYORS
PLANNING & DEVELOPMENT SPECIALISTS
1108 WEST 10th ST. CHEYENNE, WY. 82001 • (307) 634-7223
256 GILCHRIST ST. WHEATLAND, WY. 82201 • (307) 522-9729
www.StielSurvey.com • info@StielSurvey.com



SUNRISE HILLS
DRIVE (60' R/W)

SESLAR AVE

SUNRISE HILLS

SUNRISE HILLS
REPLAT

CP EAST
N=237683.08
E=773031.13

THE NORTH 140.52 FEET OF THE
SOUTH 281.04 FEET OF THE
WEST 310 FEET OF TRACT 5 and
THE WEST 200 FEET OF THE
SOUTH 140.52 FEET OF THE
WEST 310 FEET OF TRACT 5,
DELL RANGE ADDITION, CITY OF
CHEYENNE, LARAMIE COUNTY,
WYOMING.

N=243404.86'
E=765194.79'

CP RIDGE
N=245807.40
E=765234.40

DOUGLAS ST. (60' R/W)

ALLIANCE ADD.

LEGEND

- AREA TO BE ANNEXED
- EXISTING CITY LIMITS

ANNEXATION AREA

TOTAL AREA: 1.65 ACRES

ABUTTING ANNEXATION AND RATIO TO TOTAL PERIMETER - 100%


APPROVALS

Approved by the City Council of the City of Cheyenne, Wyoming,
this _____ day of _____, 2025.

Mayor


ATTEST: _____
City Clerk

BASIS OF BEARINGS:
WYOMING STATE PLANE COORDINATES,
EAST ZONE, NAD83–2011,
US SURVEY FEET, DISTANCES ARE GRID
DISTANCES.

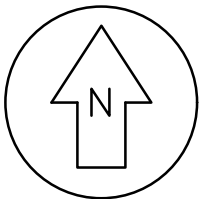

0 80'
Scale: 1"=80'

FILING RECORD

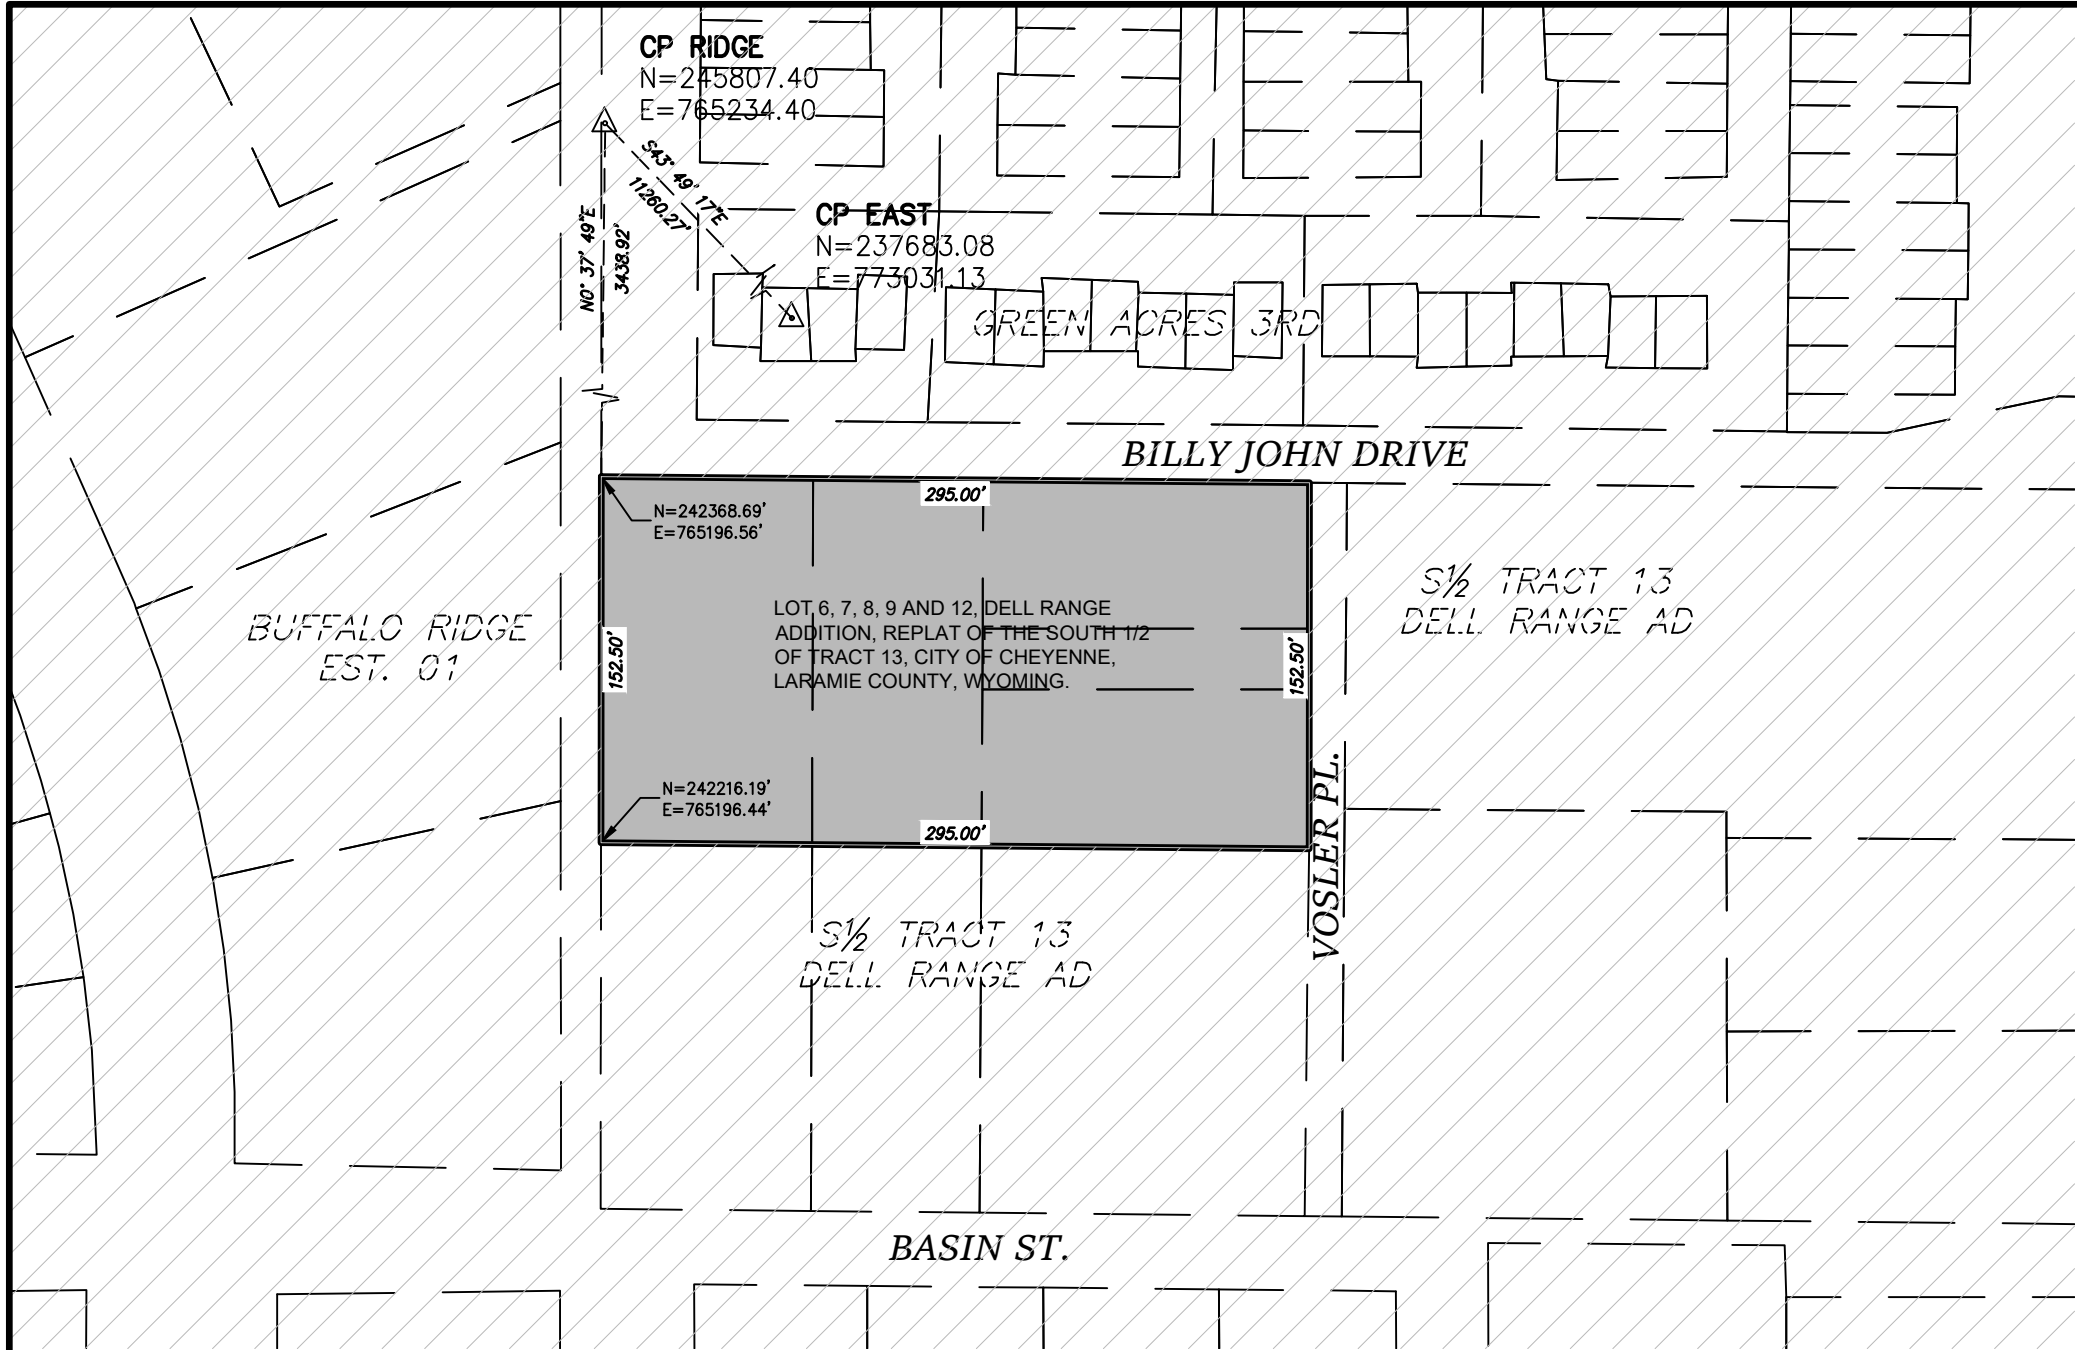

LEGEND



AREA TO BE ANNEXED



EXISTING CITY LIMITS

ANNEXATION AREA

TOTAL AREA: 0.84 ACRES

ABUTTING ANNEXATION AND RATIO TO TOTAL PERIMETER - 100%

APPROVALS

Approved by the City Council of the City of Cheyenne, Wyoming, this _____ day of _____, 2025.

Mayor

ATTEST: _____
City Clerk

FILING RECORD

--


CERTIFICATE OF SURVEYOR

I, JEFFREY B. JONES, A PROFESSIONAL LAND SURVEYOR IN THE STATE OF WYOMING, HEREBY STATE THAT THESE ANNEXATION MAPS WERE PREPARED FROM OFFICIAL PLATS AND DEEDS OF RECORD AND FROM NOTES OF A SURVEY CONDUCTED BY MYSELF OR UNDER MY DIRECT SUPERVISION DURING THE MONTHS OF FEBRUARY –JUNE, 2025, AND THAT THIS MAP CORRECTLY REPRESENTS SAID SURVEY OF THE LAND DEPICTED HEREON TO THE BEST OF MY KNOWLEDGE.

ANNEXATION DESCRIPTION - E

LOT 6, 7, 8, 9 AND 12, DELL RANGE ADDITION, REPLAT OF THE SOUTH 1/2 OF TRACT 13, CITY OF CHEYENNE, LARAMIE COUNTY, WYOMING.

BASIS OF BEARINGS:
WYOMING STATE PLANE COORDINATES, EAST ZONE, NAD83–2011, US SURVEY FEET, DISTANCES ARE GRID DISTANCES.

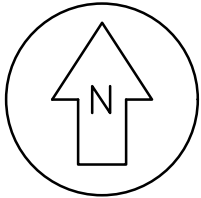

0 80'
Scale: 1"=80'





CERTIFICATE OF SURVEYOR


I, JEFFREY B. JONES, A PROFESSIONAL LAND SURVEYOR IN THE STATE OF WYOMING, HEREBY STATE THAT THESE ANNEXATION MAPS WERE PREPARED FROM OFFICIAL PLATS AND DEEDS OF RECORD AND FROM NOTES OF A SURVEY CONDUCTED BY MYSELF OR UNDER MY DIRECT SUPERVISION DURING THE MONTHS OF FEBRUARY – JUNE, 2025, AND THAT THIS MAP CORRECTLY REPRESENTS SAID SURVEY OF THE LAND DEPICTED HEREON TO THE BEST OF MY KNOWLEDGE.

ANNEXATION DESCRIPTION - F


All that portion of Tract 20, Dell Range Addition, being a subdivision of the west half of Section 22, Township 14 North, Range 66 West of the 6th P.M., Laramie County, Wyoming, described as follows:

Beginning at a point of the east boundary of a parcel of land described in that certain Deed recorded in Book 1061 at Page 297 of the Laramie County Records which point bears S.0°32.5'E. a distance of 105.0 feet from a point on the north boundary of said Tract 20 from which the northeast corner thereof bears East a distance of 123.4 feet (124 feet in Book 1061 at Page thence s. 0°32.5 E. along said east boundary a distance of 45.0 feet to the southeast corner of said parcel of land marked by rebar with an aluminum I.D. Cap attached; thence S. 89°59'W. along the south boundary of said parcel of land a distance of 124.5 feet (124 feet in Book 1061 at Page 297) to a point marked by a rebar with an aluminum I.D. Cap attached; thence N 0°30'W. along the west boundary of said parcel of land a distance of 45.0 feet to a point marked by a No.5 rebar with an aluminum I.D. Cap attached; thence N 89°59'E. a distance of 124.5 feet to the point of beginning.

BASIS OF BEARINGS:
WYOMING STATE PLANE COORDINATES,
EAST ZONE, NAD83–2011,
US SURVEY FEET, DISTANCES ARE GRID
DISTANCES.

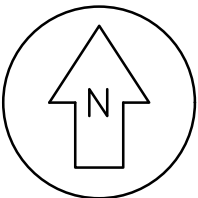

0 80'
Scale: 1"=80'

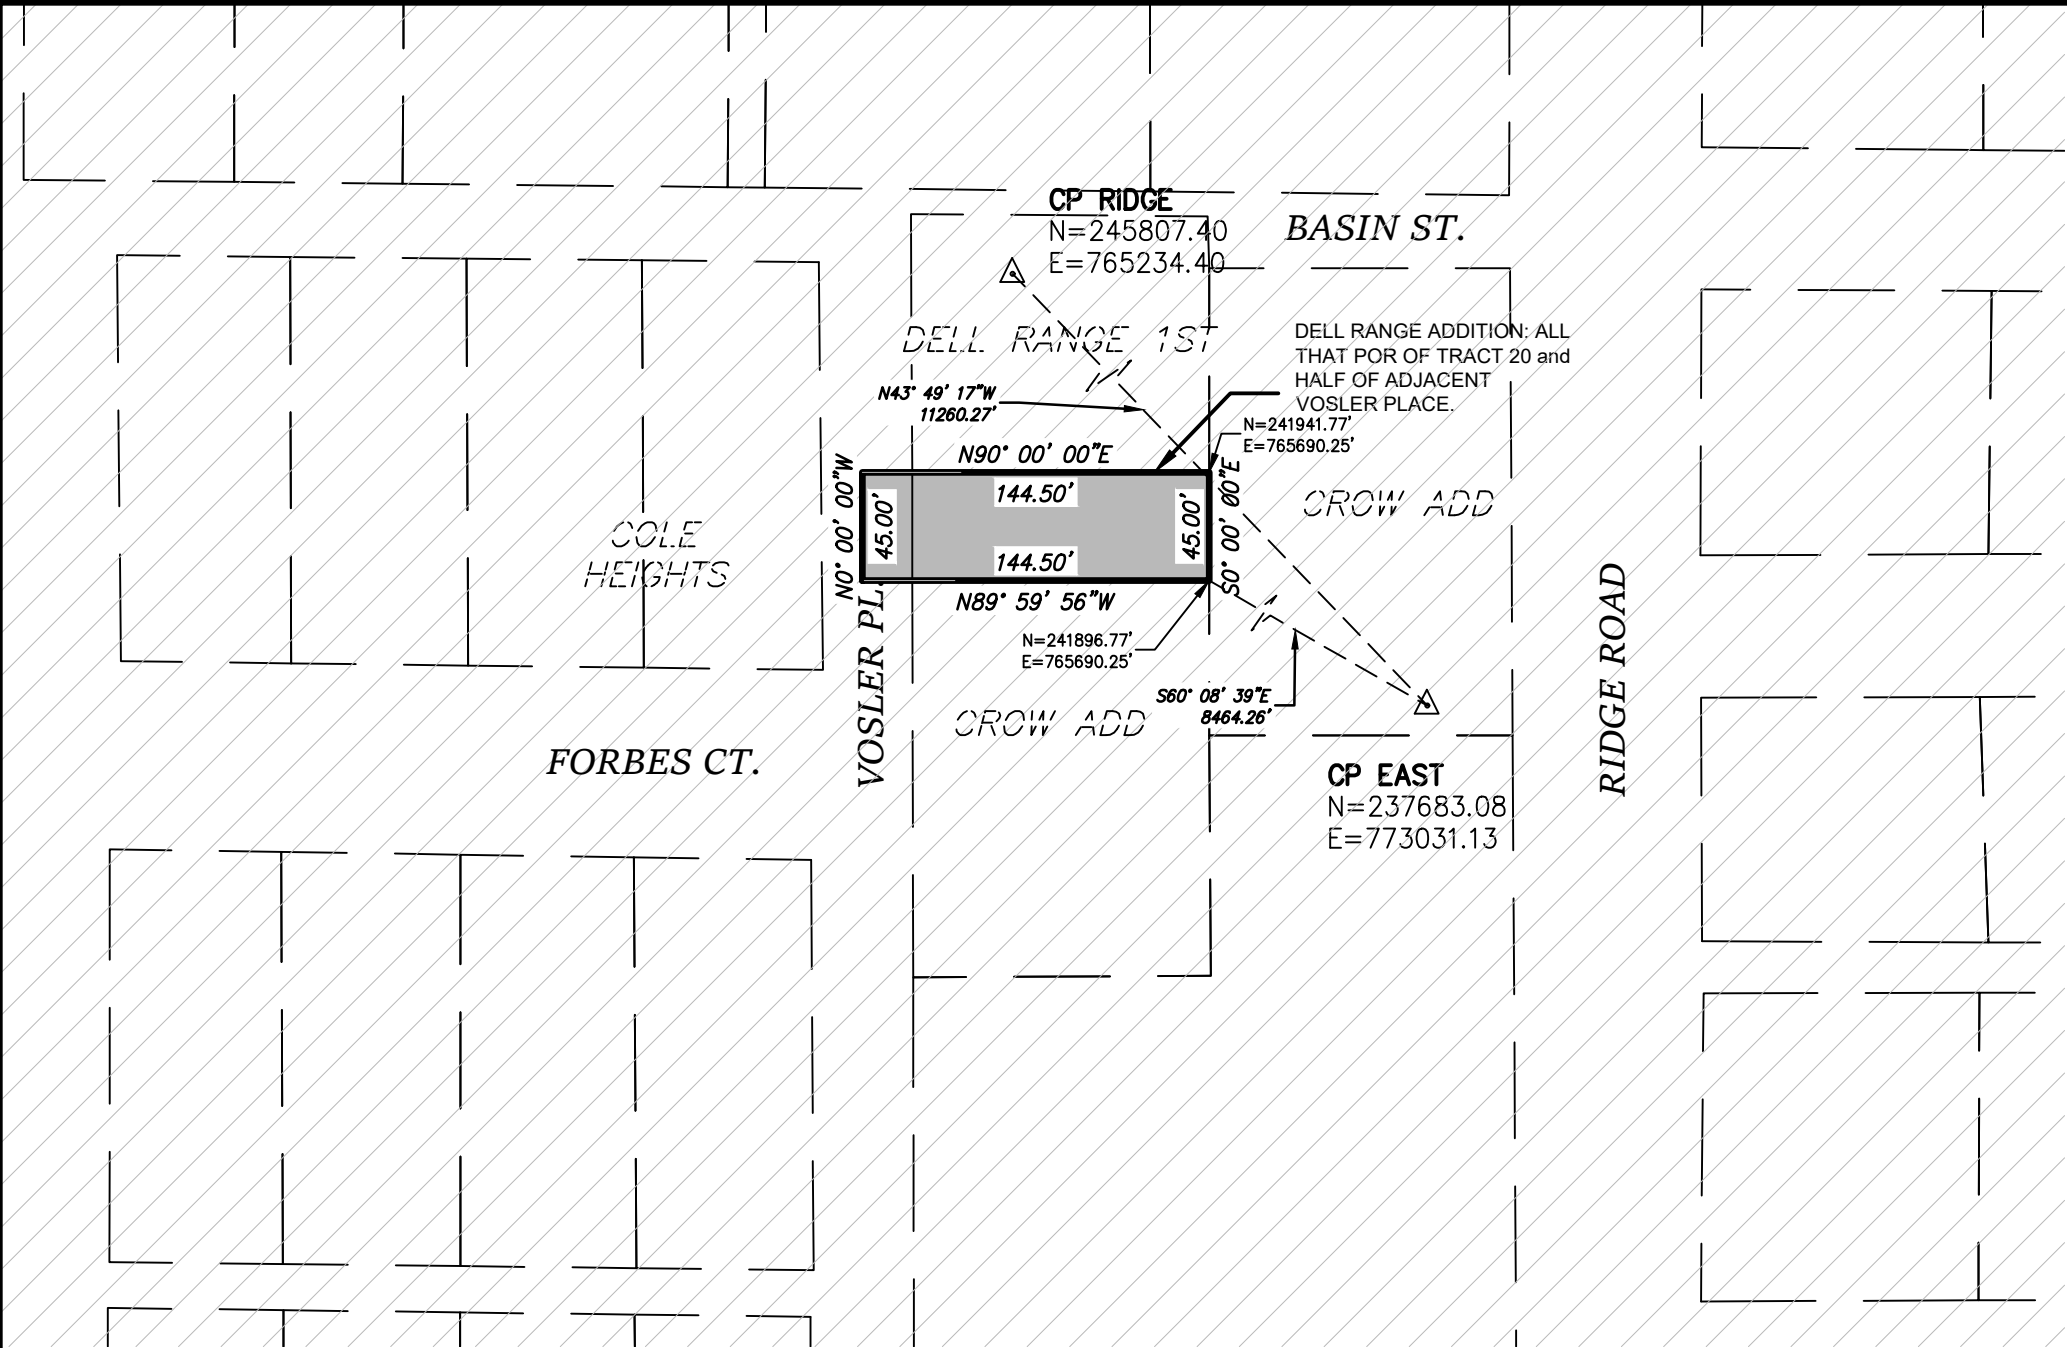

LEGEND

-  AREA TO BE ANNEXED
-  EXISTING CITY LIMITS

ANNEXATION AREA

TOTAL AREA: 0.15 ACRES
ABUTTING ANNEXATION AND RATIO TO TOTAL PERIMETER - 100%

APPROVALS

Approved by the City Council of the City of Cheyenne, Wyoming,
this _____ day of _____, 2025.

Mayor

ATTEST: _____
City Clerk

FILING RECORD




CERTIFICATE OF SURVEYOR

I, JEFFREY B. JONES, A PROFESSIONAL LAND SURVEYOR IN THE STATE OF WYOMING, HEREBY STATE THAT THESE ANNEXATION MAPS WERE PREPARED FROM OFFICIAL PLATS AND DEEDS OF RECORD AND FROM NOTES OF A SURVEY CONDUCTED BY MYSELF OR UNDER MY DIRECT SUPERVISION DURING THE MONTHS OF FEBRUARY –JUNE, 2025, AND THAT THIS MAP CORRECTLY REPRESENTS SAID SURVEY OF THE LAND DEPICTED HEREON TO THE BEST OF MY KNOWLEDGE.

ANNEXATION DESCRIPTION - G

LOT 5, COLE HEIGHTS ADDITION and THE ADJACENT 60' RIGHT OF WAY OF COLE PLACE, CITY OF CHEYENNE, LARAMIE COUNTY, WYOMING.

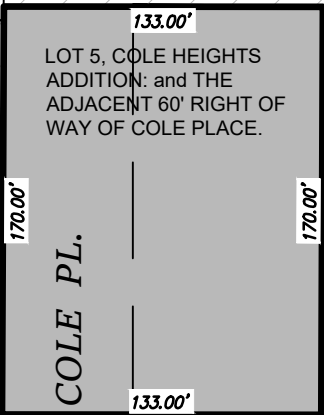

N=241783.58'
E=765311.54'

CP RIDGE
N=245807.40
E=765234.40

N43° 49' 17"W
11260.27'

N=241613.58'
E=765310.57'

S63° 01' 10"E
8663.48'

CP EAST
N=237683.08
E=773031.13

LEGEND



AREA TO BE ANNEXED



EXISTING CITY LIMITS

ANNEXATION AREA

TOTAL AREA: 0.50 ACRES

ABUTTING ANNEXATION AND RATIO TO TOTAL PERIMETER - 100%

APPROVALS

Approved by the City Council of the City of Cheyenne, Wyoming,
this _____ day of _____, 2025.


Mayor

ATTEST:

City Clerk

FILING RECORD

BASIS OF BEARINGS:
WYOMING STATE PLANE COORDINATES,
EAST ZONE, NAD83–2011,
US SURVEY FEET, DISTANCES ARE GRID
DISTANCES.

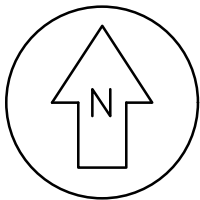

0 80'

Scale: 1"=80'

CERTIFICATE
OF
SURVEYOR


SHEET #
8 OF 9

I, JEFFREY B. JONES, A PROFESSIONAL LAND SURVEYOR IN THE STATE OF WYOMING, HEREBY STATE THAT THESE ANNEXATION MAPS WERE PREPARED FROM OFFICIAL PLATS AND DEEDS OF RECORD AND FROM NOTES OF A SURVEY CONDUCTED BY MYSELF OR UNDER MY DIRECT SUPERVISION DURING THE MONTHS OF FEBRUARY –JUNE, 2025, AND THAT THIS MAP CORRECTLY REPRESENTS SAID SURVEY OF THE LAND DEPICTED HEREON TO THE BEST OF MY KNOWLEDGE.

COUNTY POCKETS
FORCED ANNEXATION
NUMBER 5 – EXHIBIT H

REVISED: 5/1/2025
25112 EXHIBIT H.DWG

STEEL SURVEYING SERVICES, LLC
PROFESSIONAL LAND SURVEYORS
PLANNING & DEVELOPMENT SPECIALISTS
1108 WEST 19th ST. CHEYENNE, WY. 82001 • (307) 634-7223
256 GILCHRIST ST. WHEATLAND, WY. 82201 • (307) 582-9789
www.SteelSurvey.com • info@SteelSurvey.com

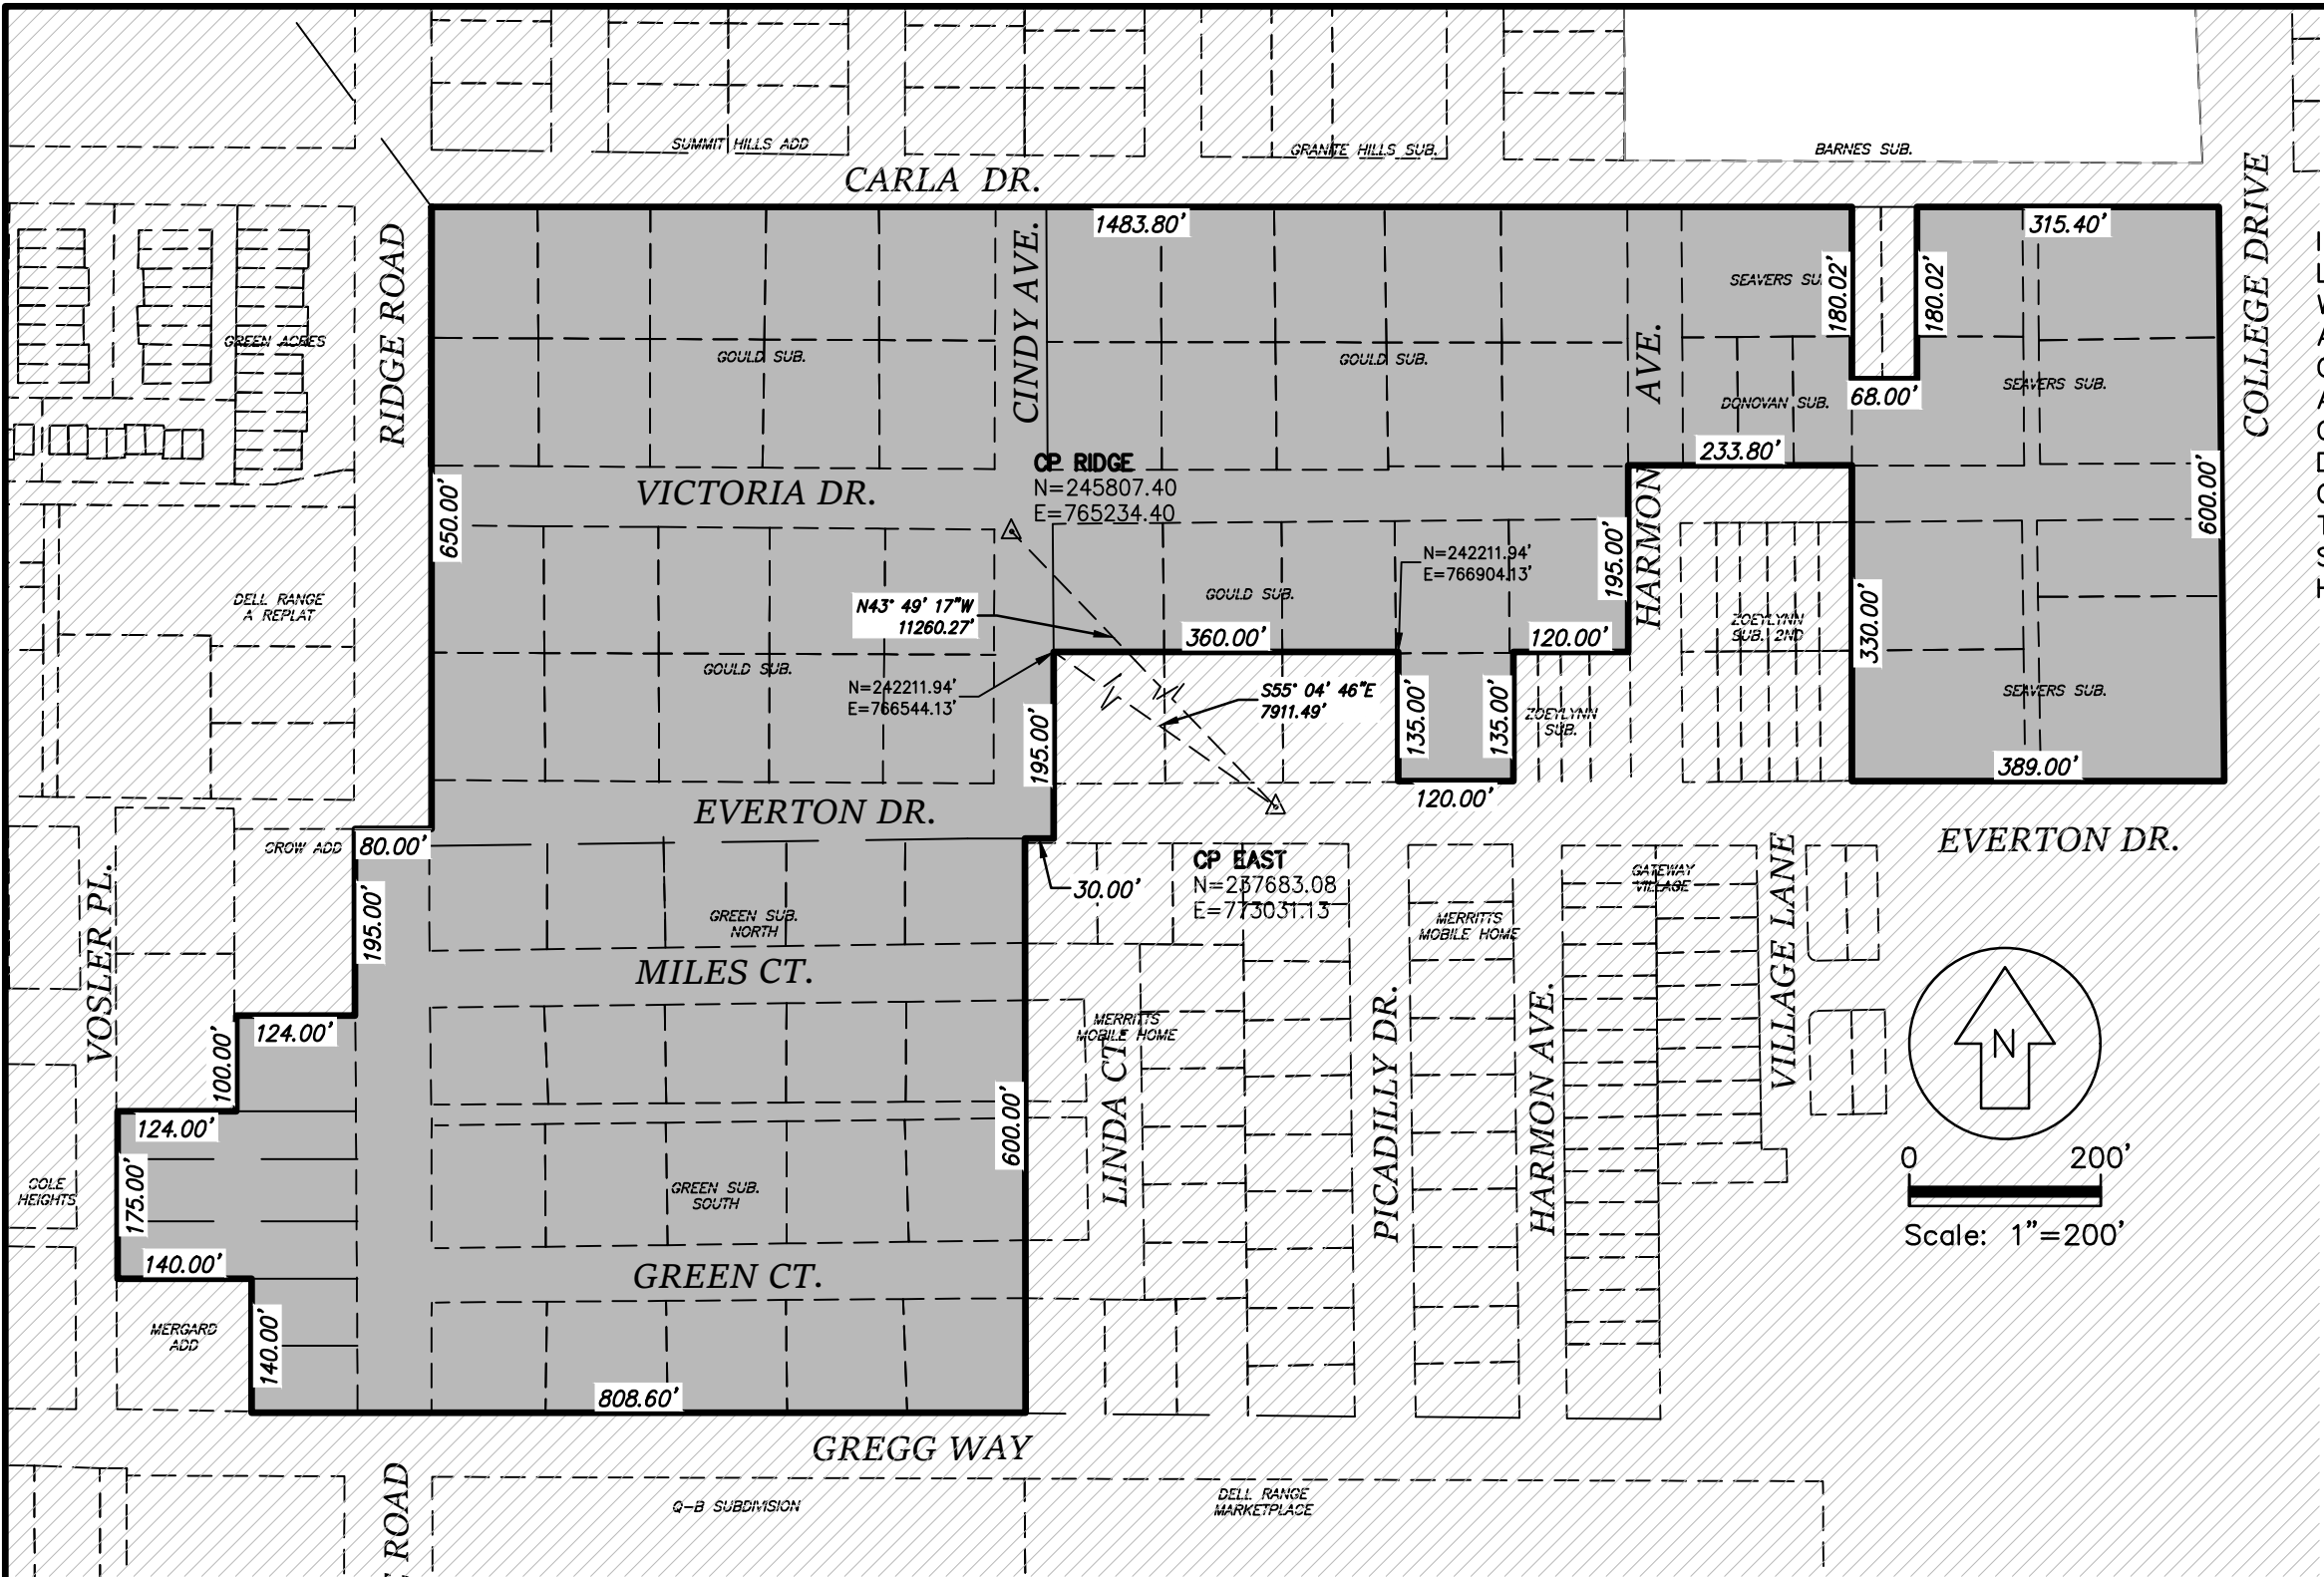

BASIS OF BEARINGS:
WYOMING STATE PLANE COORDINATES,
EAST ZONE, NAD83–2011,
US SURVEY FEET, DISTANCES ARE GRID
DISTANCES.

LEGEND

- AREA TO BE ANNEXED
- EXISTING CITY LIMITS

ANNEXATION AREA

TOTAL AREA: 34.17 ACRES
ABUTTING ANNEXATION AND RATIO TO TOTAL PERIMETER - 100%

APPROVALS

Approved by the City Council of the City of Cheyenne, Wyoming,
this _____ day of _____, 2025.

Mayor _____ ATTEST: _____
City Clerk

FILING RECORD

Pidn: AS OF 4-7-25	Pidn: AS OF 4-7-25	Pidn: AS OF 4-7-25	Pidn: AS OF 4-7-25	Pidn: AS OF 4-7-25	Pidn: AS OF 4-7-25	Pidn: AS OF 4-7-25	Pidn: AS OF 4-7-25
14662111905000	14662231200500	14662111905000	14662231001200	14662231400500	14662231800700	14662233700100	14662232700900
14662231000400	14662231200400	14662231000400	14662231500300	14662231401300	14662231800600	14662232001000	14662232700700
14662231000300	14662231201900	14662231000300	14662231500900	14662231401200	14662231800500	14662232001100	14662232700400
14662231000200	14662231200100	14662231000200	14662231501000	14662231400300	14662232000200	14662232001200	14662232700600
14662231001000	14662231200900	14662231001000	14662231500400	14662231400200	14662232000300	14662231802800	14662232700500
14662231000900	14662231201100	14662231000900	14662231500500	14662231400100	14662232000400	14662231802900	14662231300100
14662231100400	14662231201000	14662231100400	14662231500600	14662231400700	14662232000500	14662231803000	14662231300600
14662231100300	14662231201500	14662231100300	14662231500700	14662231400800	14662232000600	14662231803100	14662231300200
14662231100200	14662231201400	14662231100200	14662231501100	14662231800900	14662232000700	14662231803200	14662231300300
14662231100100	14662231201300	14662231100100	14662231500800	14662231800800	14662232001800	14662232701000	14662231300500
							14048000200090

ANNEXATION DESCRIPTION - H

ALL PARCELS AND PLATTED RIGHTS OF WAY LOCATED WITHIN: BEGINNING AT THE SOUTHWEST CORNER OF LOT 5, BLOCK 4, GOULD SUBDIVISION, THENCE SOUTHERLY ALONG THE EASTERLY RIGHT OF WAY OF CINDY AVE. A DISTANCE OF 195.00 FEET TO A POINT ON THE SOUTHERLY RIGHT OF WAY OF EVERTON DR.; THENCE WESTERLY ALONG SAID RIGHT OF WAY 30.00 FEET TO THE NORTHEASTERLY CORNER OF TRACT 20 OF GREEN SUBDIVISION OF THE NORTH HALF OF TRACT 19, DELL RANGE ADDITION; THENCE SOUTHERLY A DISTANCE OF 600.00 FEET ALONG THE EASTERLY BOUNDARIES OF GREEN SUBDIVISIONS OF BOTH THE NORTH HALF AND SOUTH HALF OF TRACT 19, DELL RANGE ADDITION TO A POINT ON THE NORTHERLY RIGHT OF WAY OF GREGG WAY; THENCE WESTERLY ALONG SAID RIGHT OF WAY A DISTANCE OF 700.60 FEET TO THE SOUTHEASTERLY CORNER OF TRACT 20, DELL RANGE ADDITION; THENCE INCLUSIVE OF EXISTING PARCELS BEING PORTIONS OF TRACT 20, DELL RANGE ADDITION DESCRIBED AS CONTINUING WESTERLY ALONG SAID RIGHT OF WAY A DISTANCE OF 108 FEET TO A POINT; THENCE NORTHERLY 140.00 FEET TO A POINT; THENCE WESTERLY 140.00 FEET TO A POINT ON THE EASTERLY RIGHT OF WAY OF VOSLER PLACE; THENCE NORTHERLY ALONG SAID RIGHT OF WAY 175.00 FEET TO THE SOUTHWESTERLY CORNER OF LOT 1, BLOCK 1, CROW ADDITION; THENCE ALONG THE BOUNDARY OF SAID CROW ADDITION THE FOLLOWING FOUR COURSES; THENCE EASTERLY A DISTANCE OF 124.00 FEET TO A POINT; THENCE NORTHERLY 100 FEET TO A POINT; THENCE EASTERLY 124.00 FEET TO A POINT ON THE WESTERLY RIGHT OF WAY OF RIDGE ROAD; THENCE NORTHERLY ALONG SAID RIGHT OF WAY A DISTANCE OF 195.00 FEET TO THE POINT OF INTERSECTION WITH THE SOUTHERLY RIGHT OF WAY OF BASIN STREET EXTENDED; THENCE EASTERLY 80.00 FEET TO A POINT ON THE EASTERLY RIGHT OF WAY OF RIDGE ROAD; THENCE NORTHERLY ALONG SAID RIGHT OF WAY, BEING THE WESTERLY BOUNDARY OF GOULD SUBDIVISION, A DISTANCE OF 650 FEET TO THE NORTHWESTERLY CORNER OF LOT 5, BLOCK 2, GOULD SUBDIVISION; THENCE EASTERLY ALONG THE SOUTHERLY RIGHT OF WAY OF CARLA DRIVE A DISTANCE OF 1483.80 FEET TO THE NORTHEASTERLY CORNER OF LOT 5, BLOCK 1, SEAVER SUBDIVISION; THENCE THE FOLLOWING THREE COURSES ALONG THE BOUNDARIES OF SEILOFF ADDITION, THENCE SOUTHERLY 180.02 FEET; THENCE EASTERLY 68.00 FEET; THENCE NORTHERLY 180.02 FEET TO THE SOUTHERLY RIGHT OF WAY OF CARLA DRIVE; THENCE CONTINUING EASTERLY ALONG SAID SOUTHERLY RIGHT OF WAY A DISTANCE OF 315.40 FEET TO THE NORTHEASTERLY CORNER OF LOT 1, BLOCK 1, SEAVERS SUBDIVISION; THENCE SOUTHERLY ALONG THE WESTERLY RIGHT OF WAY OF COLLEGE DRIVE A DISTANCE OF 600.00 FEET TO THE SOUTHEASTERLY CORNER OF LOT 2, BLOCK 2, SEAVERS SUBDIVISION; THENCE WESTERLY 389.00 FEET ALONG THE NORTHERLY RIGHT OF WAY OF EVERTON DRIVE TO THE SOUTHWESTERLY CORNER OF LOT 3, BLOCK 2, SEAVERS SUBDIVISION; THENCE NORTHERLY 330.00 FEET TO THE SOUTHEASTERLY CORNER OF DONOVAN SUBDIVISION; THENCE WESTERLY A DISTANCE OF 233.80 FEET ALONG THE NORTHERLY RIGHT OF WAY OF VICTORIA DRIVE TO THE SOUTHEASTERLY CORNER OF LOT 2, BLOCK 1, GOULD SUBDIVISION 2ND FILING; THENCE SOUTHERLY A DISTANCE OF 195.00 FEET TO THE SOUTHEASTERLY CORNER OF LOT 1, BLOCK 4, GOULD SUBDIVISION; THENCE WESTERLY A DISTANCE OF 120.00 FEET TO THE SOUTHWESTERLY CORNER OF SAID LOT 1, BLOCK 4, GOULD SUBDIVISION; THENCE SOUTHERLY A DISTANCE OF 135.00 FEET TO THE SOUTHEASTERLY CORNER OF LOT 9, BLOCK 4, GOULD SUBDIVISION; THENCE WESTERLY A DISTANCE OF 120.00 FEET ALONG THE NORTHERLY RIGHT OF WAY OF EVERTON DRIVE TO THE SOUTHWESTERLY CORNER OF SAID LOT 9; THENCE NORTHERLY A DISTANCE OF 135.00 FEET TO THE NORTHWESTERLY CORNER OF SAID LOT 9; THENCE WESTERLY A DISTANCE OF 360.00 FEET TO THE POINT OF BEGINNING.

FILING RECORD

COUNTY POCKETS
FORCED ANNEXATION
NUMBER 5 – EXHIBIT H

REVISED: 4/11/2025
25112 EXHIBIT H.DWG

STIEL SURVEYING SERVICES, LLC
PROFESSIONAL LAND SURVEYORS
PLANNING & DEVELOPMENT SPECIALISTS
1108 WEST 10th ST. CHEYENNE, WY. 82001 • (307) 634-7223
256 GILCHRIST ST. WHEATLAND, WY. 82001 • (307) 582-3739
www.StielSurvey.com • info@StielSurvey.com





A COMMUNITY OF CHOICE

Planning and Development Department

2101 O'Neil Avenue, Suite 202, Cheyenne WY 82001

(Phone) 307-637-6282 (Fax) 307-637-6366

CITY OF CHEYENNE GOVERNING BODY

MAY 27, 2025

STAFF REPORT


FILE: PUDC-25-50: County Pocket #5 - Annexation

REQUEST: An annexation of 95 properties 100% surrounded by the City.

LOCATION: North of Dell Range Boulevard, east and west of Ridge Road and south of Storey Boulevard.

PURPOSE: Annexation of County pockets is a 2022 City Council priority.

PREPARED BY: Connor White, Planner II

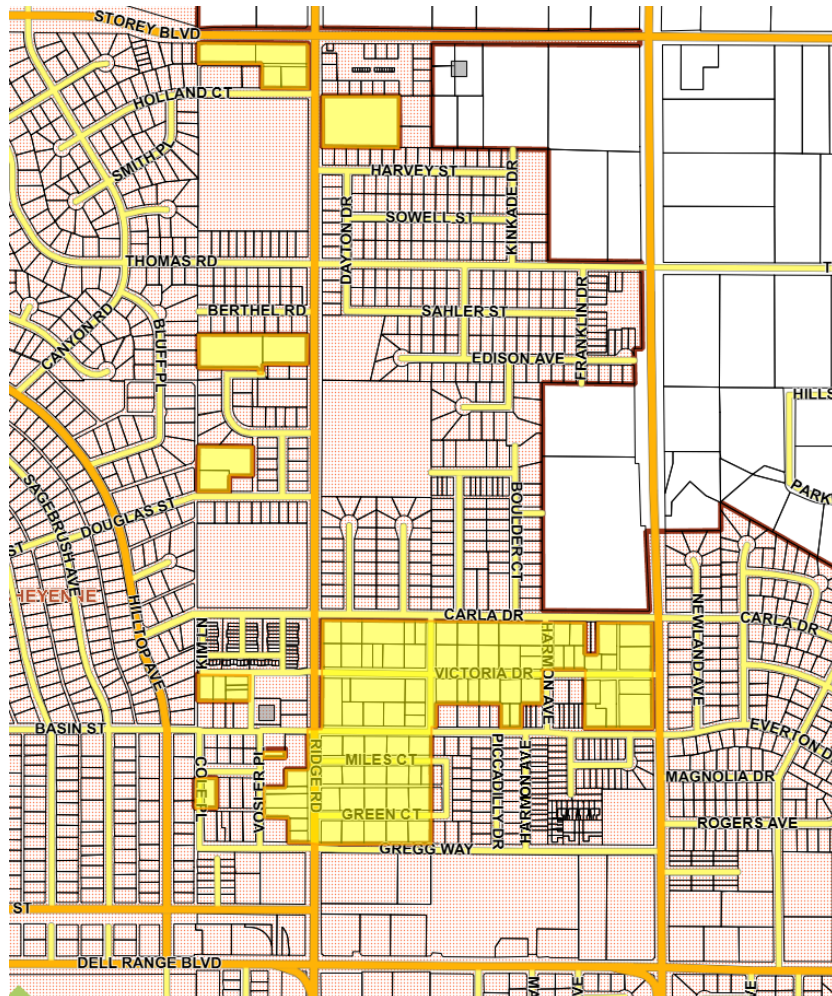

APPLICABLE CITY CODE SECTION(S) AND PLANS:

- UDC 2.4.2 Annexations
- PlanCheyenne

BACKGROUND:

Annexation of County pockets is a 2022 City Council priority. A “County pocket” is an area of unincorporated land 100% surrounded by the City of Cheyenne. City-initiated annexations do not require an owner’s signature. To initiate an annexation, the City must adopt a resolution certifying that the annexation complies with Wyoming State Statute § 15-1-402. After the City adopts this resolution, the annexation follows the typical schedule, including a public hearing and the approval of an Ordinance which annexes the land. The Governing Body adopted Resolution No. 6432 initiating this annexation on October 28, 2023.

This annexation is comprised of 95 properties 100% surrounded by the City (See attached map). Of the 95 parcels, a majority are developed with residential uses, several are developed with commercial uses and others are undeveloped or incorporated into adjacent parcels under similar ownership.

Land annexed to the City requires a City zone. An assigned zoning ordinance is accompanying this annexation to assign the AG, MR, MUR and CB zones.

ANALYSIS OF APPLICATION CONFORMANCE WITH REVIEW CRITERIA:

To approve the annexation Ordinance, the Governing Body must make the following findings required in WS 15-1-402; a detailed analysis of which is below:

1) An annexation of the area is for the protection of the health, safety and welfare of the persons residing in the area and in the city or town. [WS 15-1-402 (a) (i)]

The annexation of these properties will increase the health, safety, and welfare of the future occupants. By being in City limits, the property will receive access to City Fire and Police and sanitation services. The properties will also have the option of connecting to City water and sanitary sewer instead of having wells and septic systems.

The application **complies** with this review criterion.

2) The urban development of the area sought to be annexed would constitute a natural, geographical, economical and social part of the annexing city or town. [WS 15-1-402 (a) (ii)]

These properties constitute a natural, geographic, economic, and social part of the city. The properties are surrounded by City on all sides. The contiguity to the City and the proximity to surrounding urban-style development makes the parcels a natural geographic part of the City.

The application **complies** with this review criterion.

- 3) The area sought to be annexed is a logical and feasible addition to the annexing city or town and the extension of basic and other services customarily available to residents of the city or town shall, within reason, be available to the area proposed to be annexed. [WS 15-1-402 (a) (iii)]**

The area is a logical and feasible addition to the City due to the reasons previously listed. All City services normally available to residents will also be made available. There are properties that are already connected to City water and sewer within the area to be annexed. Police and fire protection will be extended upon annexation. Utilities exist in the area and will be expanded into the proposed area as they redevelop.

The application **complies** with this review criterion.

- 4) The area sought to be annexed is contiguous with or adjacent to the annexing city or town, or the area meets the requirements of W.S. 15-1-407. [WS 15-1-402 (a) (iv)]**

The area proposed for annexation is 100% contiguous on all sides.

The application **complies** with this review criterion.

- 5) If the city or town does not own or operate its own electric utility, its governing body is prepared to issue one (1) or more franchises as necessary to serve the annexed area pursuant to W.S. 15-1-410. [WS 15-1-402 (a) (v)]**

Utility franchises are in place to serve the annexed area.

The application **complies** with this review criterion.

- 6) The annexing city or town, not less than twenty (20) business days prior to the public hearing required by W.S. 15-1-405(a), has sent by certified mail to all landowners and affected public utilities within the territory and by first class mail to any persons owning property that is adjacent to or within three hundred (300) feet of the territory proposed to be annexed, regardless of whether the property is inside or outside the corporate limits of the annexing city or town and regardless of whether the city or town is exercising authority under W.S. 15-3-202(b)(ii), a summary of the proposed annexation report as required under subsection (c) of this section and notice of the time, date and location of the public hearing required by W.S. 15-1-405(a). [WS 15-1-402 (a) (vi)]**

A certified mailing was made to the landowners and public utilities on April 25, 2025. Neighbors within 300' were mailed first-class letters on April 23, 24, and 25. The public hearing for this annexation is scheduled for May 27, 2025. Twenty (20) business days (on the City's calendar) prior to the announced public hearing is April 28, 2025. The earliest confirmation of delivery was dated April 28, 2025.

The application **complies** with this review criterion.

CONFORMANCE WITH APPLICABLE PLANS:

The project is located in an area covered by the following plans:

- Plan Cheyenne

The Future Land Use Map of PlanCheyenne, as updated by Connect 2045, anticipates this area of the community to develop with urban residential uses and a little bit of Mixed-use Commercial uses. These areas are expected to develop with full access to urban services – such areas are best served by being within City limits. The area is within the Urban Service Boundary.

STAFF REVIEW:

Through the review process, no comments were received.

CONCLUSION:

Staff is satisfied that the application meets the review criteria and therefore recommends approval of the annexation.


The proposed annexation is a natural extension of the City, is contiguous to the current City limits, and most services typically available to urban areas are available to be extended to this property.



STAFF RECOMMENDATION:

Staff recommends approval of the annexation.

ATTACHMENTS:

1. Current Zoning Map
2. Future Land Use Map
3. Annexation map

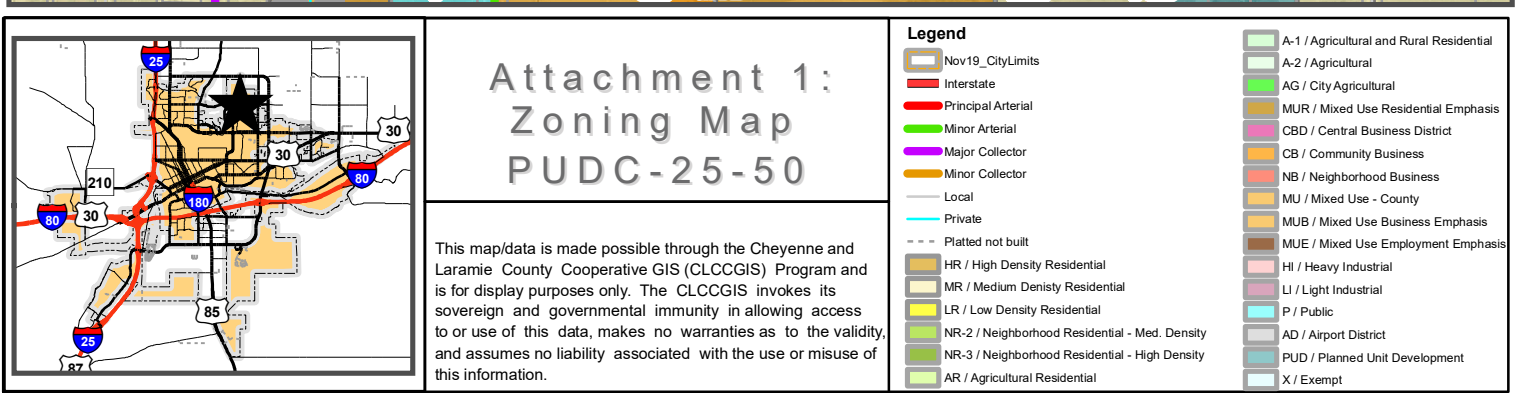

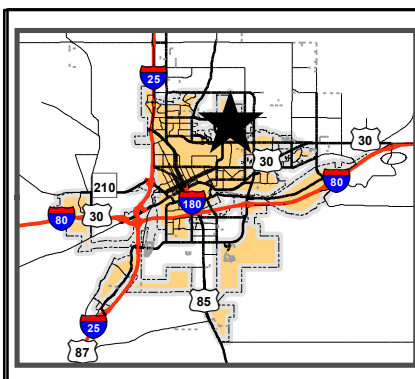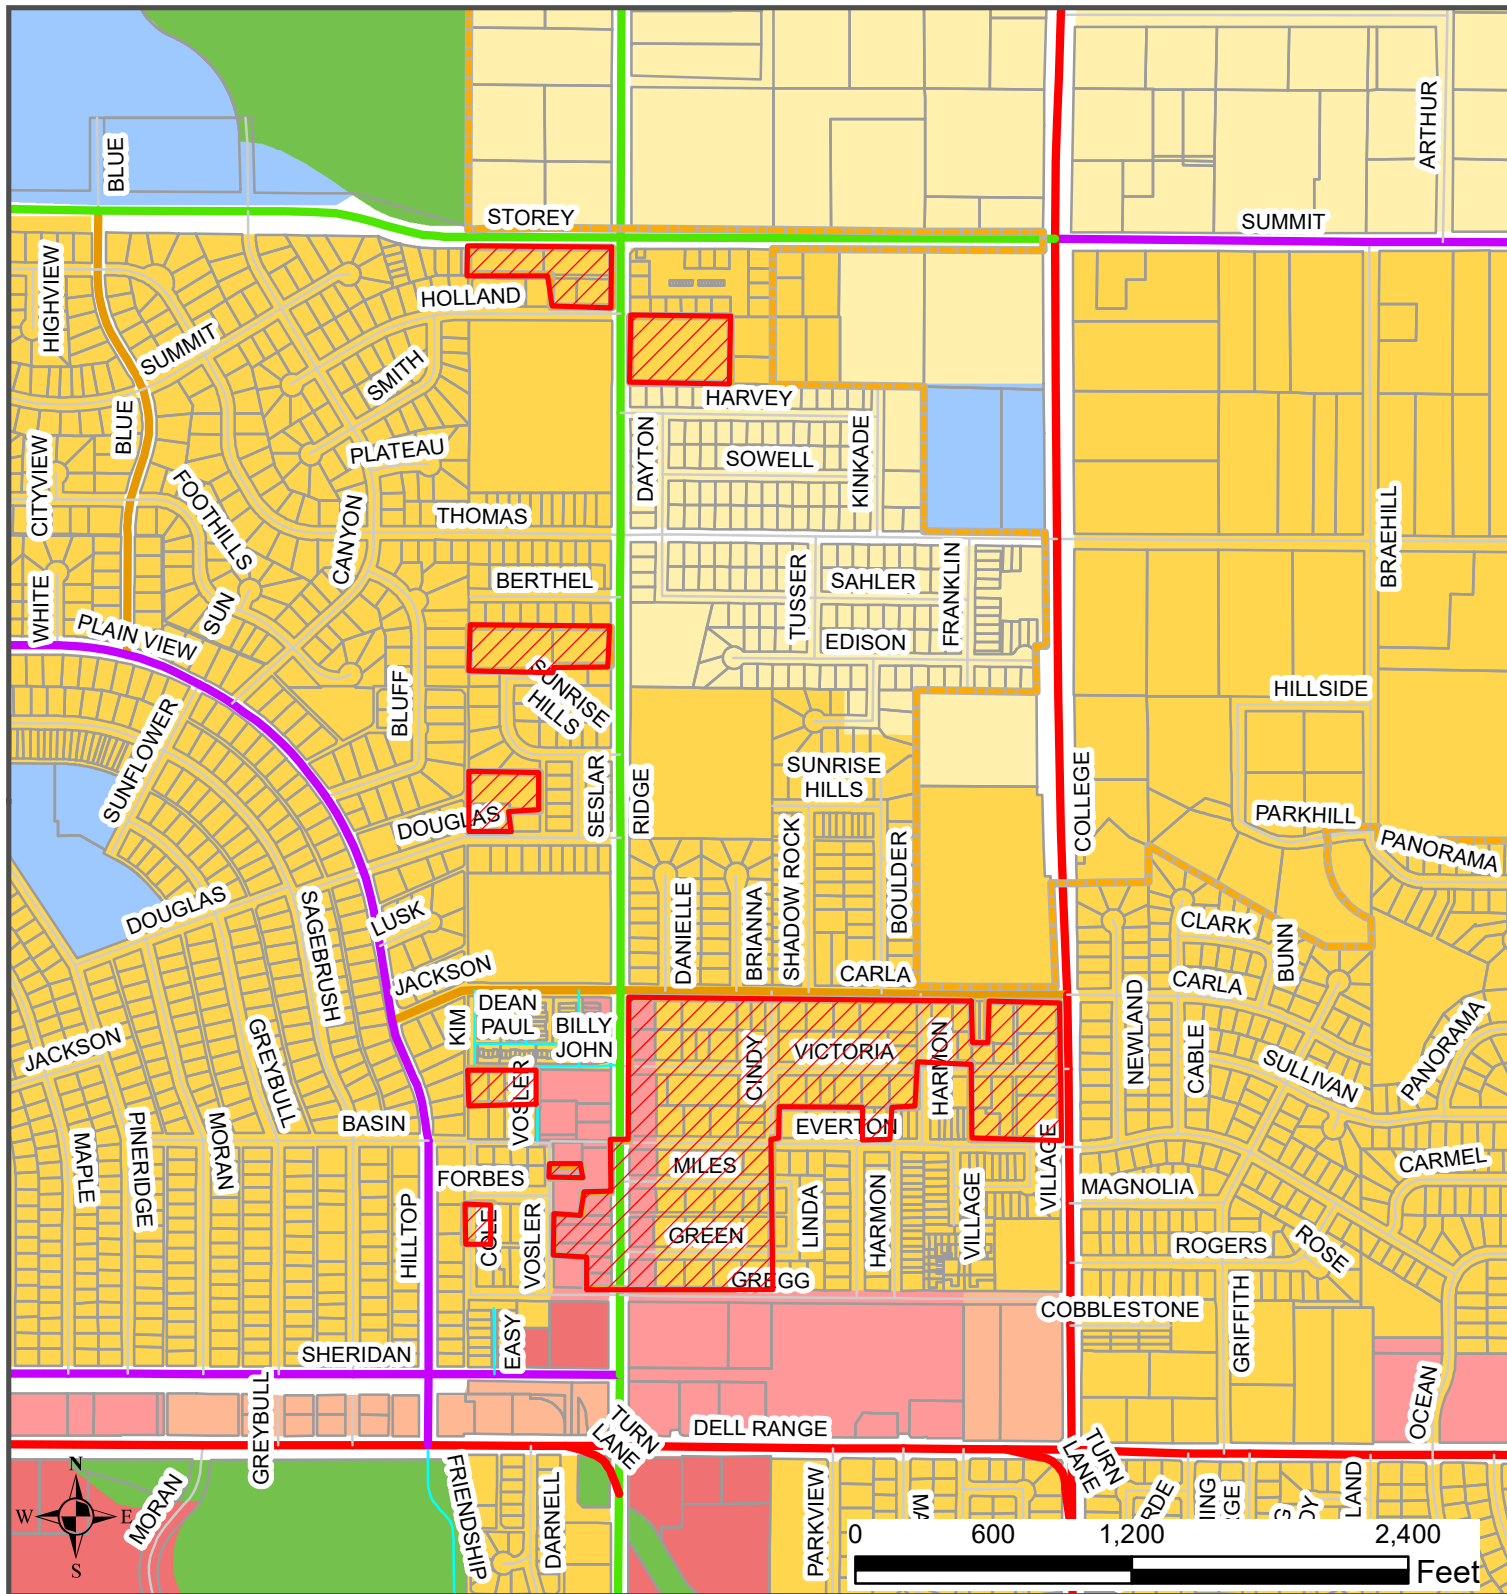

Attachment 2: Land Use Map PUDC-25-50

This map/data is made possible through the Cheyenne and Laramie County Cooperative GIS (CLCCGIS) Program and is for display purposes only. The CLCCGIS invokes its sovereign and governmental immunity in allowing access to or use of this data, makes no warranties as to the validity, and assumes no liability associated with the use or misuse of this information.

Legend

City Limits	Agricultural/Rural	Industrial
Interstate	Rural Residential	Central Business District
Principal Arterial	Urban Transition Residential	Community Business
Minor Arterial	Urban Residential	Public and Quasi-Public
Major Collector	Mixed-Use Residential	Military/Federal
Minor Collector	Mixed-Use Commercial	Open Space and Parks
Local	Mixed-Use Employment	
Private		
Platted not built		
Ownership		

ANNEXATION MAP
COUNTY POCKETS
FORCED ANNEXATION #5

SHEET #
1 OF 9



COUNTY POCKETS
FORCED ANNEXATION
NUMBER 5

REVISED: 4/11/2025
25112 VMAP.DWG

STEEL SURVEYING SERVICES, LLC
PROFESSIONAL LAND SURVEYORS
PLANNING & DEVELOPMENT SPECIALISTS
1108 WEST 19th ST. CHEYENNE, WY. 82001 • (307) 634-7223
256 GILCHRIST ST. WHEATLAND, WY. 82201 • (307) 582-9789
www.SteelSurvey.com • info@SteelSurvey.com



BASIS OF BEARINGS:
WYOMING STATE PLANE COORDINATES,
EAST ZONE, NAD83-2011,
US SURVEY FEET, DISTANCES ARE GRID
DISTANCES.

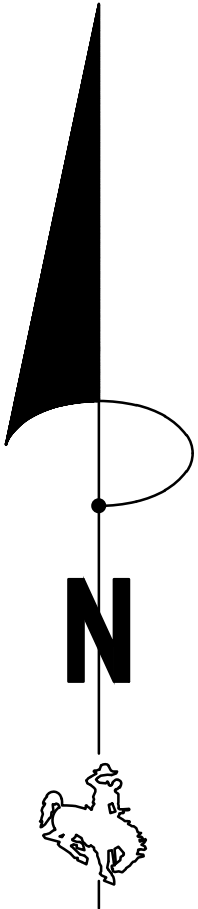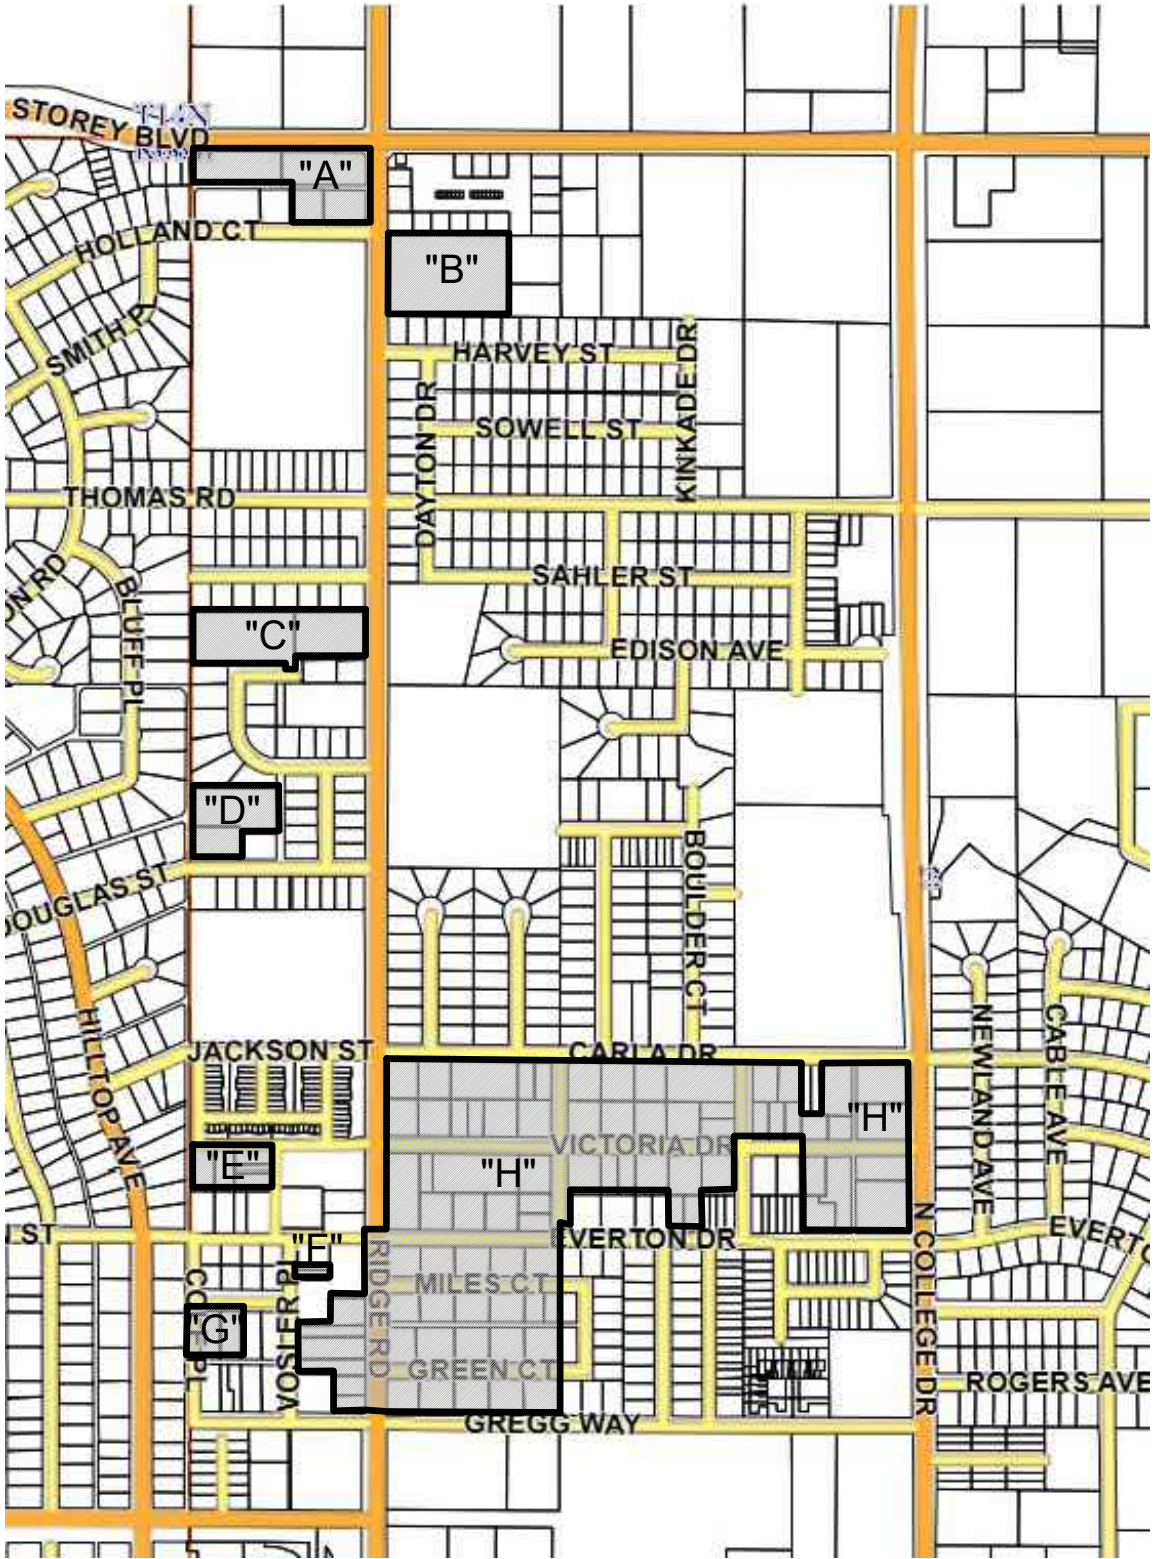

FILING RECORD

VICINITY MAP
(NOT TO SCALE)

PREPARED APRIL 2025

CERTIFICATE OF SURVEYOR

I, JEFFREY B. JONES, A PROFESSIONAL LAND SURVEYOR IN THE STATE OF WYOMING, HEREBY STATE THAT THESE ANNEXATION MAPS WERE PREPARED FROM OFFICIAL PLATS AND DEEDS OF RECORD AND FROM NOTES OF A SURVEY CONDUCTED BY MYSELF OR UNDER MY DIRECT SUPERVISION DURING THE MONTHS OF FEBRUARY –JUNE, 2025, AND THAT THIS MAP CORRECTLY REPRESENTS SAID SURVEY OF THE LAND DEPICTED HEREON TO THE BEST OF MY KNOWLEDGE.

CERTIFICATE OF SURVEYOR

I, JEFFREY B. JONES, A PROFESSIONAL LAND SURVEYOR IN THE STATE OF WYOMING, HEREBY STATE THAT THESE ANNEXATION MAPS WERE PREPARED FROM OFFICIAL PLATS AND DEEDS OF RECORD AND FROM NOTES OF A SURVEY CONDUCTED BY MYSELF OR UNDER MY DIRECT SUPERVISION DURING THE MONTHS OF FEBRUARY-JUNE, 2025, AND THAT THIS MAP CORRECTLY REPRESENTS SAID SURVEY OF THE LAND DEPICTED HEREON TO THE BEST OF MY KNOWLEDGE.


COUNTY POCKETS
FORCED ANNEXATION
NUMBER 5
EXHIBIT A

ANNEXATION DESCRIPTION - A

Tracts 1 thru 8, 30 feet of vacated Grove Avenue, Tract 13 except the west 36 feet, Tracts 14, 15 and 16, Block 1 and the 16' alley adjacent thereto, Holland Smith Subdivision, City of Cheyenne, Laramie County, Wyoming.

REVISED: 5/1/2025
25112 EXHIBIT A.DWG

STEL SURVEYING SERVICES, LLC
PROFESSIONAL LAND SURVEYORS
PLANNING & DEVELOPMENT SPECIALISTS
1108 WEST 10th ST. CHEYENNE, WY. 82001 • (307) 634-7223
256 GILCHRIST ST. WHEATLAND, WY. 82201 • (307) 522-9729
www.StelSurvey.com • info@StelSurvey.com

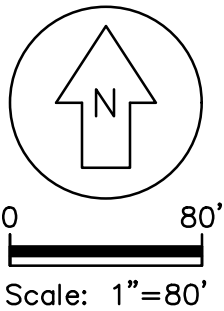

PIDN: AS OF 4-6-25
14662220201500
14662220200700
14662220201100
14662220200600

STOREY BLVD. (90' R/W)

RIDGE ROAD (80' R/W)

HOLLAND CT. (60' R/W)

ANNEXATION AREA

TOTAL AREA: 2.66 ACRES
ABUTTING ANNEXATION AND RATIO TO TOTAL PERIMETER - 100%

APPROVALS

Approved by the City Council of the City of Cheyenne, Wyoming, this _____ day of _____, 2025.

Mayor ATTEST: _____
City Clerk

LEGEND

- AREA TO BE ANNEXED
- EXISTING CITY LIMITS

FILING RECORD


HOLLAND-SMITH
SUB.

HOLLAND CT.
(60' R/W)

DELL RANGE
ADD
PORTION
T25

RIDGE ROAD (80' R/W)

SUMMIT PARK

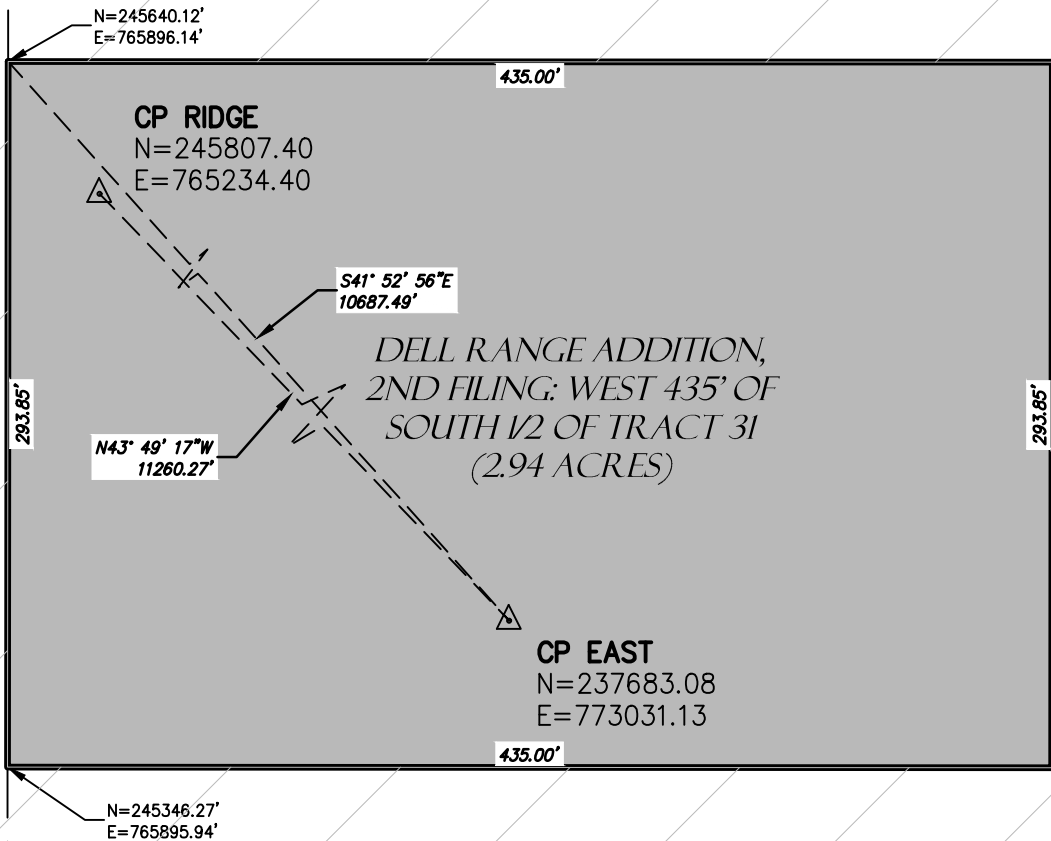

THOMAS HEIGHTS

LEGEND



AREA TO BE ANNEXED



EXISTING CITY LIMITS

ANNEXATION AREA

TOTAL AREA: 2.94 ACRES

ABUTTING ANNEXATION AND RATIO TO TOTAL
PERIMETER - 100%

FILING RECORD

APPROVALS

Approved by the City Council of the City of Cheyenne, Wyoming,
this _____ day of _____, 2025.

Mayor

ATTEST:

City Clerk


CERTIFICATE OF SURVEYOR

I, JEFFREY B. JONES, A PROFESSIONAL LAND SURVEYOR IN THE STATE OF WYOMING, HEREBY STATE THAT THESE ANNEXATION MAPS WERE PREPARED FROM OFFICIAL PLATS AND DEEDS OF RECORD AND FROM NOTES OF A SURVEY CONDUCTED BY MYSELF OR UNDER MY DIRECT SUPERVISION DURING THE MONTHS OF FEBRUARY -JUNE, 2025, AND THAT THIS MAP CORRECTLY REPRESENTS SAID SURVEY OF THE LAND DEPICTED HEREON TO THE BEST OF MY KNOWLEDGE.

ANNEXATION DESCRIPTION - B

THE WEST 435 FEET OF THE SOUTH 1/2 OF TRACT 31,
DELL RANGE ADDITION, 2ND FILING, CITY OF CHEYENNE,
LARAMIE COUNTY, WYOMING.

BASIS OF BEARINGS:
WYOMING STATE PLANE COORDINATES,
EAST ZONE, NAD83-2011,
US SURVEY FEET, DISTANCES ARE GRID
DISTANCES.

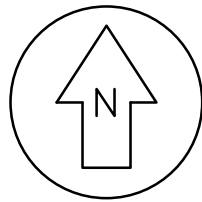

Scale: 1"=80'


SHEET #
3 OF 9

COUNTY POCKETS
FORCED ANNEXATION
NUMBER 5 - EXHIBIT B

REVISED: 4/8/2025
25112 EXHIBIT B.DWG

STIEL SURVEYING SERVICES, LLC
PROFESSIONAL LAND SURVEYORS
PLANNING & DEVELOPMENT SPECIALISTS
1108 WEST 10th ST. CHEYENNE, WY. 82001 • (307) 634-7223
256 GILCHRIST ST. WHEATLAND, WY. 82201 • (307) 522-9729
www.StielSurvey.com • info@StielSurvey.com



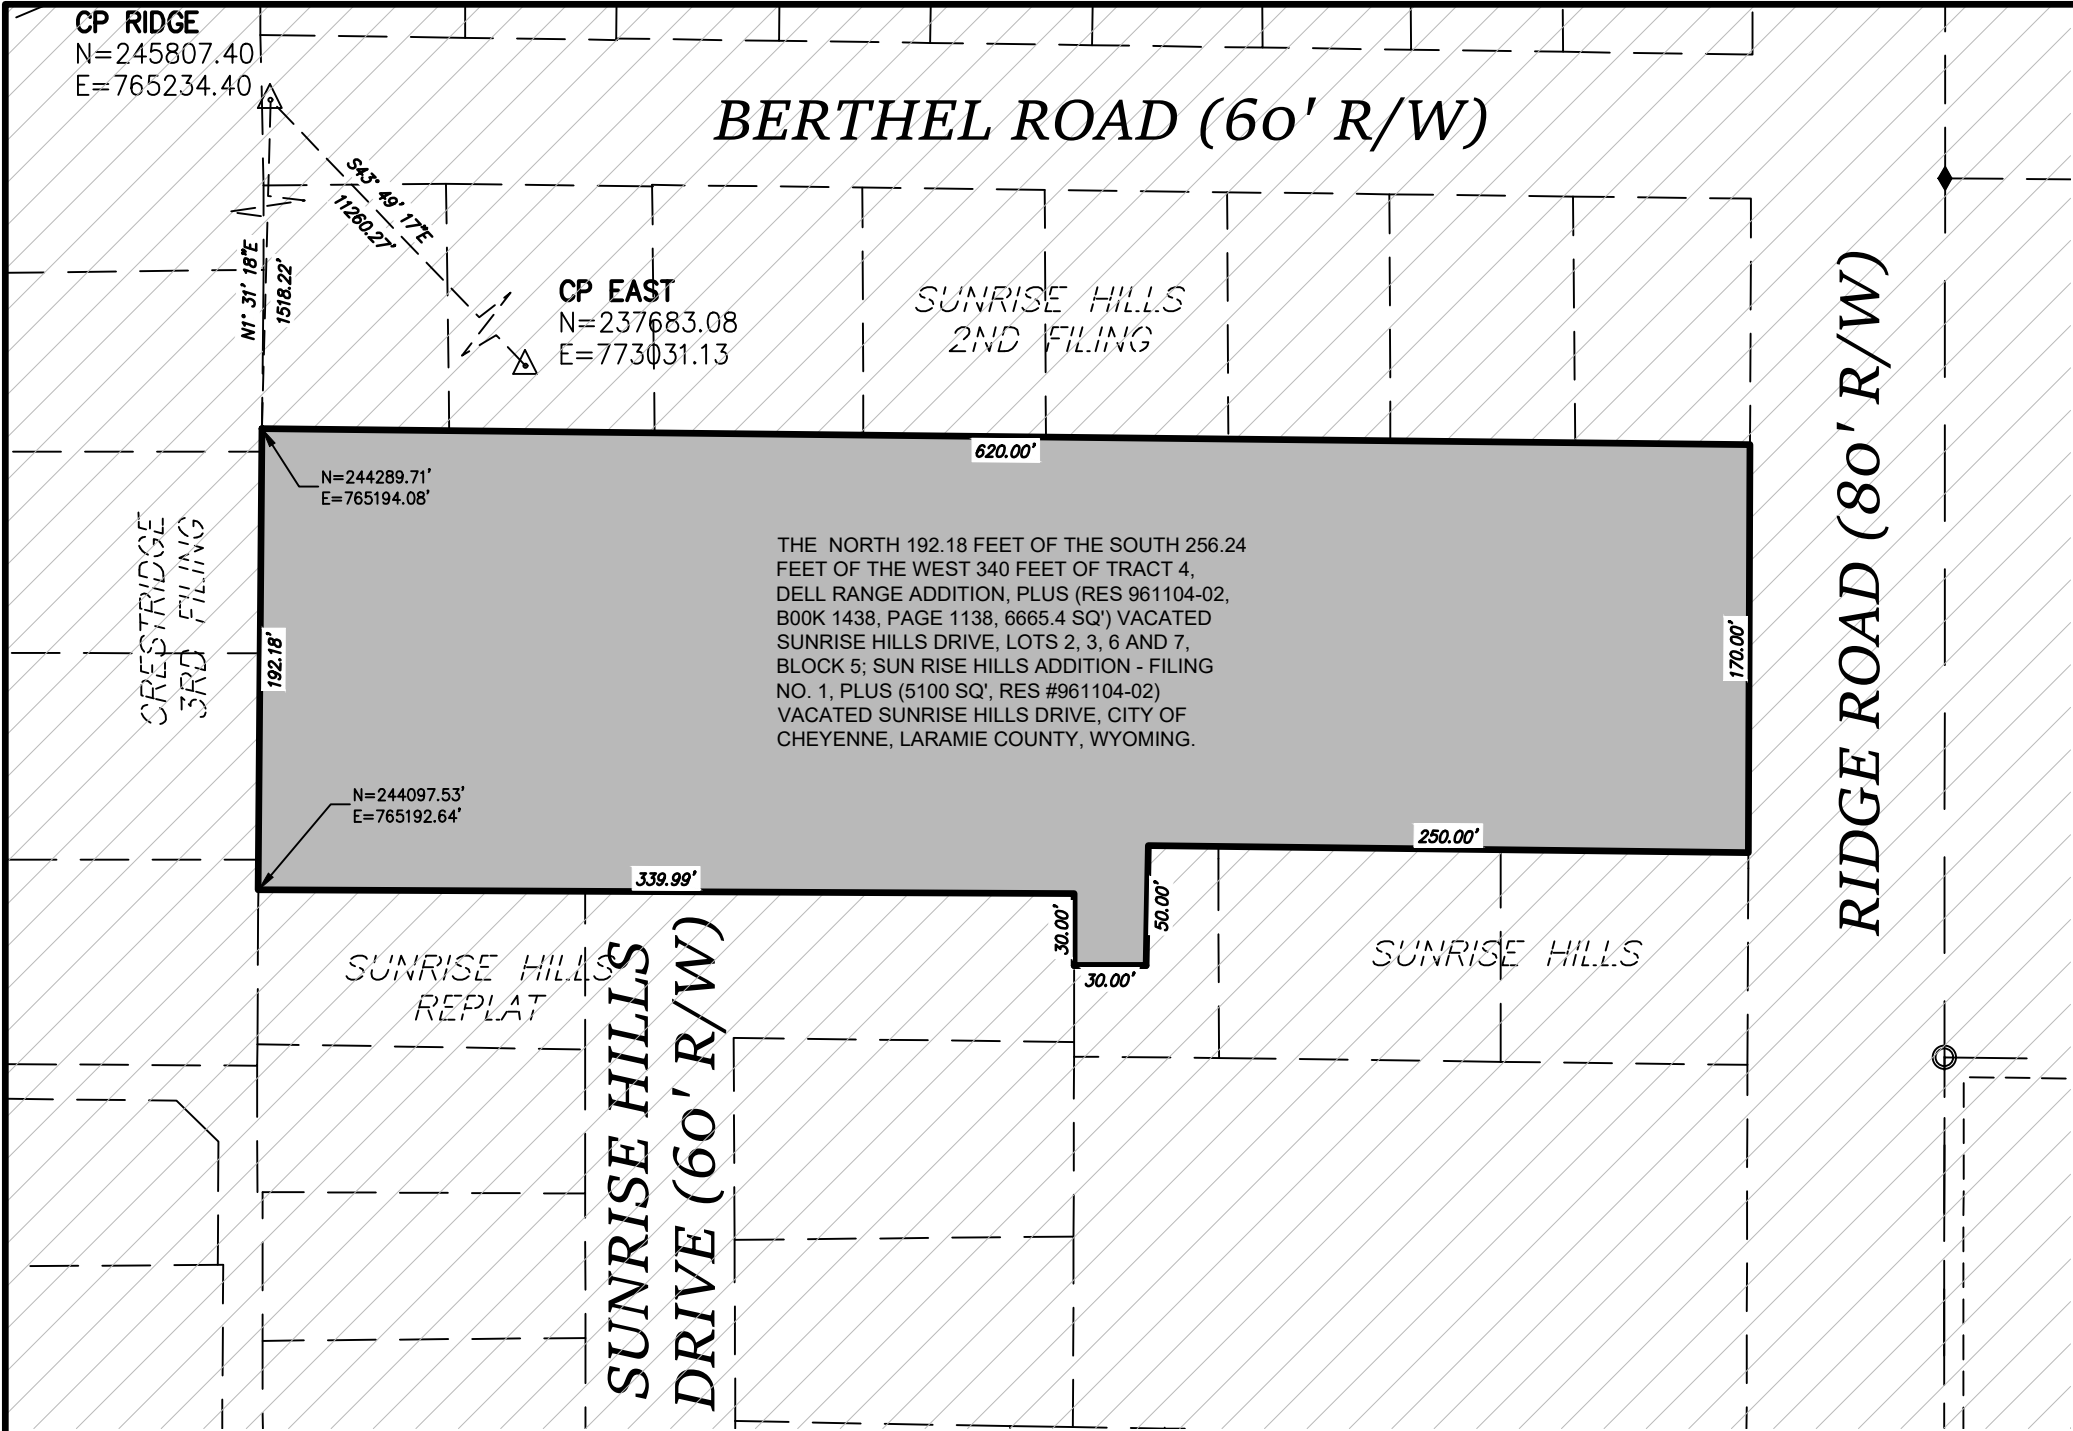

LEGEND



AREA TO BE ANNEXED



EXISTING CITY LIMITS

ANNEXATION AREA

TOTAL AREA: 1.65 ACRES

ABUTTING ANNEXATION AND RATIO TO TOTAL PERIMETER - 100%

APPROVALS

Approved by the City Council of the City of Cheyenne, Wyoming, this _____ day of _____, 2025.

Mayor

ATTEST: _____
City Clerk

FILING RECORD


CERTIFICATE OF SURVEYOR

I, JEFFREY B. JONES, A PROFESSIONAL LAND SURVEYOR IN THE STATE OF WYOMING, HEREBY STATE THAT THESE ANNEXATION MAPS WERE PREPARED FROM OFFICIAL PLATS AND DEEDS OF RECORD AND FROM NOTES OF A SURVEY CONDUCTED BY MYSELF OR UNDER MY DIRECT SUPERVISION DURING THE MONTHS OF FEBRUARY –JUNE, 2025, AND THAT THIS MAP CORRECTLY REPRESENTS SAID SURVEY OF THE LAND DEPICTED HEREON TO THE BEST OF MY KNOWLEDGE.

ANNEXATION DESCRIPTION - C

THE NORTH 192.18 FEET OF THE SOUTH 256.24 FEET OF THE WEST 340 FEET OF TRACT 4, DELL RANGE ADDITION, PLUS (RES 961104-02, B00K 1438, PAGE 1138, 6665.4 SQ') VACATED SUNRISE HILLS DRIVE, LOTS 2, 3, 6 AND 7, BLOCK 5; SUN RISE HILLS ADDITION - FILING NO. 1, PLUS (5100 SQ', RES #961104-02) VACATED SUNRISE HILLS DRIVE, CITY OF CHEYENNE, LARAMIE COUNTY, WYOMING.

BASIS OF BEARINGS:
WYOMING STATE PLANE COORDINATES,
EAST ZONE, NAD83–2011,
US SURVEY FEET, DISTANCES ARE GRID
DISTANCES.

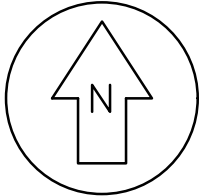

0 80'
Scale: 1"=80'



CERTIFICATE OF SURVEYOR

I, JEFFREY B. JONES, A PROFESSIONAL LAND SURVEYOR IN THE STATE OF WYOMING, HEREBY STATE THAT THESE ANNEXATION MAPS WERE PREPARED FROM OFFICIAL PLATS AND DEEDS OF RECORD AND FROM NOTES OF A SURVEY CONDUCTED BY MYSELF OR UNDER MY DIRECT SUPERVISION DURING THE MONTHS OF FEBRUARY –JUNE, 2025, AND THAT THIS MAP CORRECTLY REPRESENTS SAID SURVEY OF THE LAND DEPICTED HEREON TO THE BEST OF MY KNOWLEDGE.

ANNEXATION DESCRIPTION - D

THE NORTH 140.52 FEET OF THE SOUTH 281.04 FEET OF THE WEST 310 FEET OF TRACT 5 and THE WEST 200 FEET OF THE SOUTH 140.52 FEET OF THE WEST 310 FEET OF TRACT 5, DELL RANGE ADDITION, CITY OF CHEYENNE, LARAMIE COUNTY, WYOMING.

COUNTY POCKETS
FORCED ANNEXATION
NUMBER 5 – EXHIBIT D

REVISED: 5/1/2025
25112 EXHIBIT D.DWG

STIEL SURVEYING SERVICES, LLC
PROFESSIONAL LAND SURVEYORS
PLANNING & DEVELOPMENT SPECIALISTS
1108 WEST 10th ST. CHEYENNE, WY. 82001 • (307) 634-7223
256 GILCHRIST ST. WHEATLAND, WY. 82201 • (307) 522-9729
www.StielSurvey.com • info@StielSurvey.com



SUNRISE HILLS
DRIVE (60' R/W)

SESLAR AVE

SUNRISE HILLS

ALLIANCE ADD.

DOUGLAS ST. (60' R/W)

SUNRISE HILLS
REPLAT

BUFF RID EST
REPLAT 2

CP RIDGE
N=245807.40
E=765234.40

CP EAST
N=237683.08
E=773031.13

THE NORTH 140.52 FEET OF THE
SOUTH 281.04 FEET OF THE
WEST 310 FEET OF TRACT 5 and
THE WEST 200 FEET OF THE
SOUTH 140.52 FEET OF THE
WEST 310 FEET OF TRACT 5,
DELL RANGE ADDITION, CITY OF
CHEYENNE, LARAMIE COUNTY,
WYOMING.

N=243404.86'
E=765194.79'

310.00'

140.52'

110.00'

110.52'

200.00'

251.04'

N1° 03' 17"E

2151.86'

S43° 49' 17"E
11260.27'

LEGEND



AREA TO BE ANNEXED



EXISTING CITY LIMITS

ANNEXATION AREA

TOTAL AREA: 1.65 ACRES

ABUTTING ANNEXATION AND RATIO TO TOTAL
PERIMETER - 100%

APPROVALS

Approved by the City Council of the City of Cheyenne, Wyoming,
this ____ day of _____, 2025.


Mayor

ATTEST:


City Clerk

FILING RECORD

BASIS OF BEARINGS:
WYOMING STATE PLANE COORDINATES,
EAST ZONE, NAD83–2011,
US SURVEY FEET, DISTANCES ARE GRID
DISTANCES.

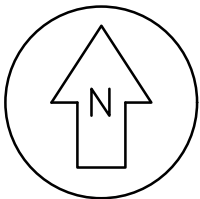

0 80'
Scale: 1"=80'

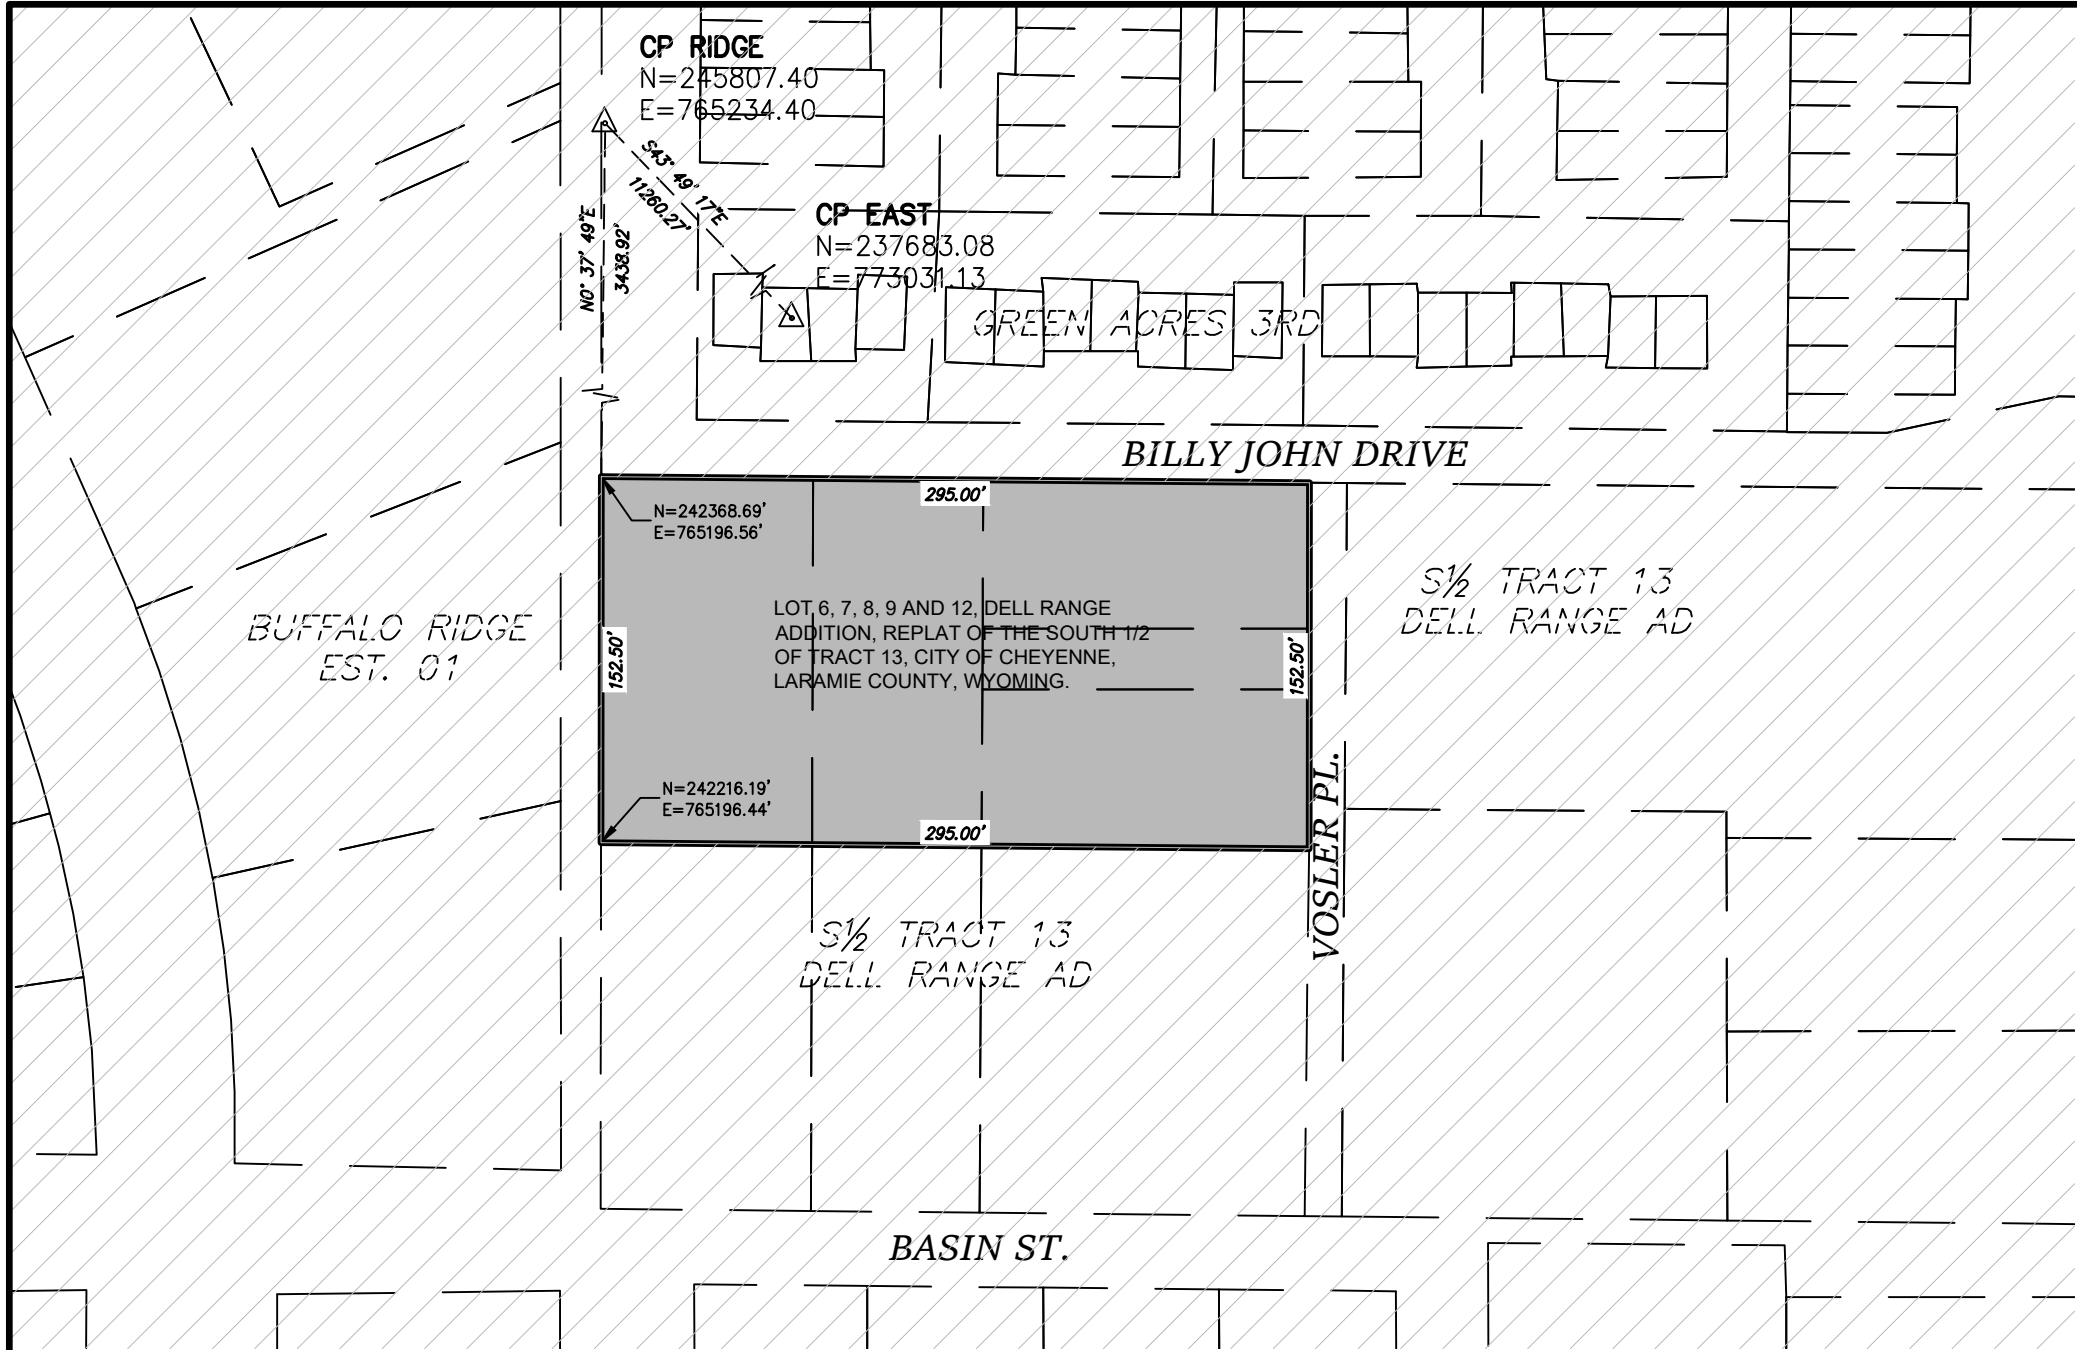

LEGEND



AREA TO BE ANNEXED



EXISTING CITY LIMITS

ANNEXATION AREA

TOTAL AREA: 0.84 ACRES

ABUTTING ANNEXATION AND RATIO TO TOTAL PERIMETER - 100%

APPROVALS

Approved by the City Council of the City of Cheyenne, Wyoming, this _____ day of _____, 2025.

Mayor

ATTEST: _____
City Clerk

FILING RECORD

--


CERTIFICATE OF SURVEYOR

I, JEFFREY B. JONES, A PROFESSIONAL LAND SURVEYOR IN THE STATE OF WYOMING, HEREBY STATE THAT THESE ANNEXATION MAPS WERE PREPARED FROM OFFICIAL PLATS AND DEEDS OF RECORD AND FROM NOTES OF A SURVEY CONDUCTED BY MYSELF OR UNDER MY DIRECT SUPERVISION DURING THE MONTHS OF FEBRUARY –JUNE, 2025, AND THAT THIS MAP CORRECTLY REPRESENTS SAID SURVEY OF THE LAND DEPICTED HEREON TO THE BEST OF MY KNOWLEDGE.

ANNEXATION DESCRIPTION - E

LOT 6, 7, 8, 9 AND 12, DELL RANGE ADDITION, REPLAT OF THE SOUTH 1/2 OF TRACT 13, CITY OF CHEYENNE, LARAMIE COUNTY, WYOMING.

BASIS OF BEARINGS:
WYOMING STATE PLANE COORDINATES,
EAST ZONE, NAD83–2011,
US SURVEY FEET, DISTANCES ARE GRID
DISTANCES.

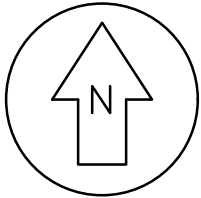

0 80'
Scale: 1"=80'





CERTIFICATE OF SURVEYOR


I, JEFFREY B. JONES, A PROFESSIONAL LAND SURVEYOR IN THE STATE OF WYOMING, HEREBY STATE THAT THESE ANNEXATION MAPS WERE PREPARED FROM OFFICIAL PLATS AND DEEDS OF RECORD AND FROM NOTES OF A SURVEY CONDUCTED BY MYSELF OR UNDER MY DIRECT SUPERVISION DURING THE MONTHS OF FEBRUARY – JUNE, 2025, AND THAT THIS MAP CORRECTLY REPRESENTS SAID SURVEY OF THE LAND DEPICTED HEREON TO THE BEST OF MY KNOWLEDGE.

ANNEXATION DESCRIPTION - F


All that portion of Tract 20, Dell Range Addition, being a subdivision of the west half of Section 22, Township 14 North, Range 66 West of the 6th P.M., Laramie County, Wyoming, described as follows:

Beginning at a point of the east boundary of a parcel of land described in that certain Deed recorded in Book 1061 at Page 297 of the Laramie County Records which point bears S.0°32.5'E. a distance of 105.0 feet from a point on the north boundary of said Tract 20 from which the northeast corner thereof bears East a distance of 123.4 feet (124 feet in Book 1061 at Page thence s. 0°32.5 E. along said east boundary a distance of 45.0 feet to the southeast corner of said parcel of land marked by rebar with an aluminum I.D. Cap attached; thence S. 89°59'W. along the south boundary of said parcel of land a distance of 124.5 feet (124 feet in Book 1061 at Page 297) to a point marked by a rebar with an aluminum I.D. Cap attached; thence N 0°30'W. along the west boundary of said parcel of land a distance of 45.0 feet to a point marked by a No.5 rebar with an aluminum I.D. Cap attached; thence N 89°59'E. a distance of 124.5 feet to the point of beginning.

BASIS OF BEARINGS:
WYOMING STATE PLANE COORDINATES,
EAST ZONE, NAD83–2011,
US SURVEY FEET, DISTANCES ARE GRID
DISTANCES.

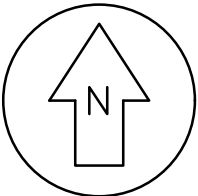

0 80'
Scale: 1"=80'

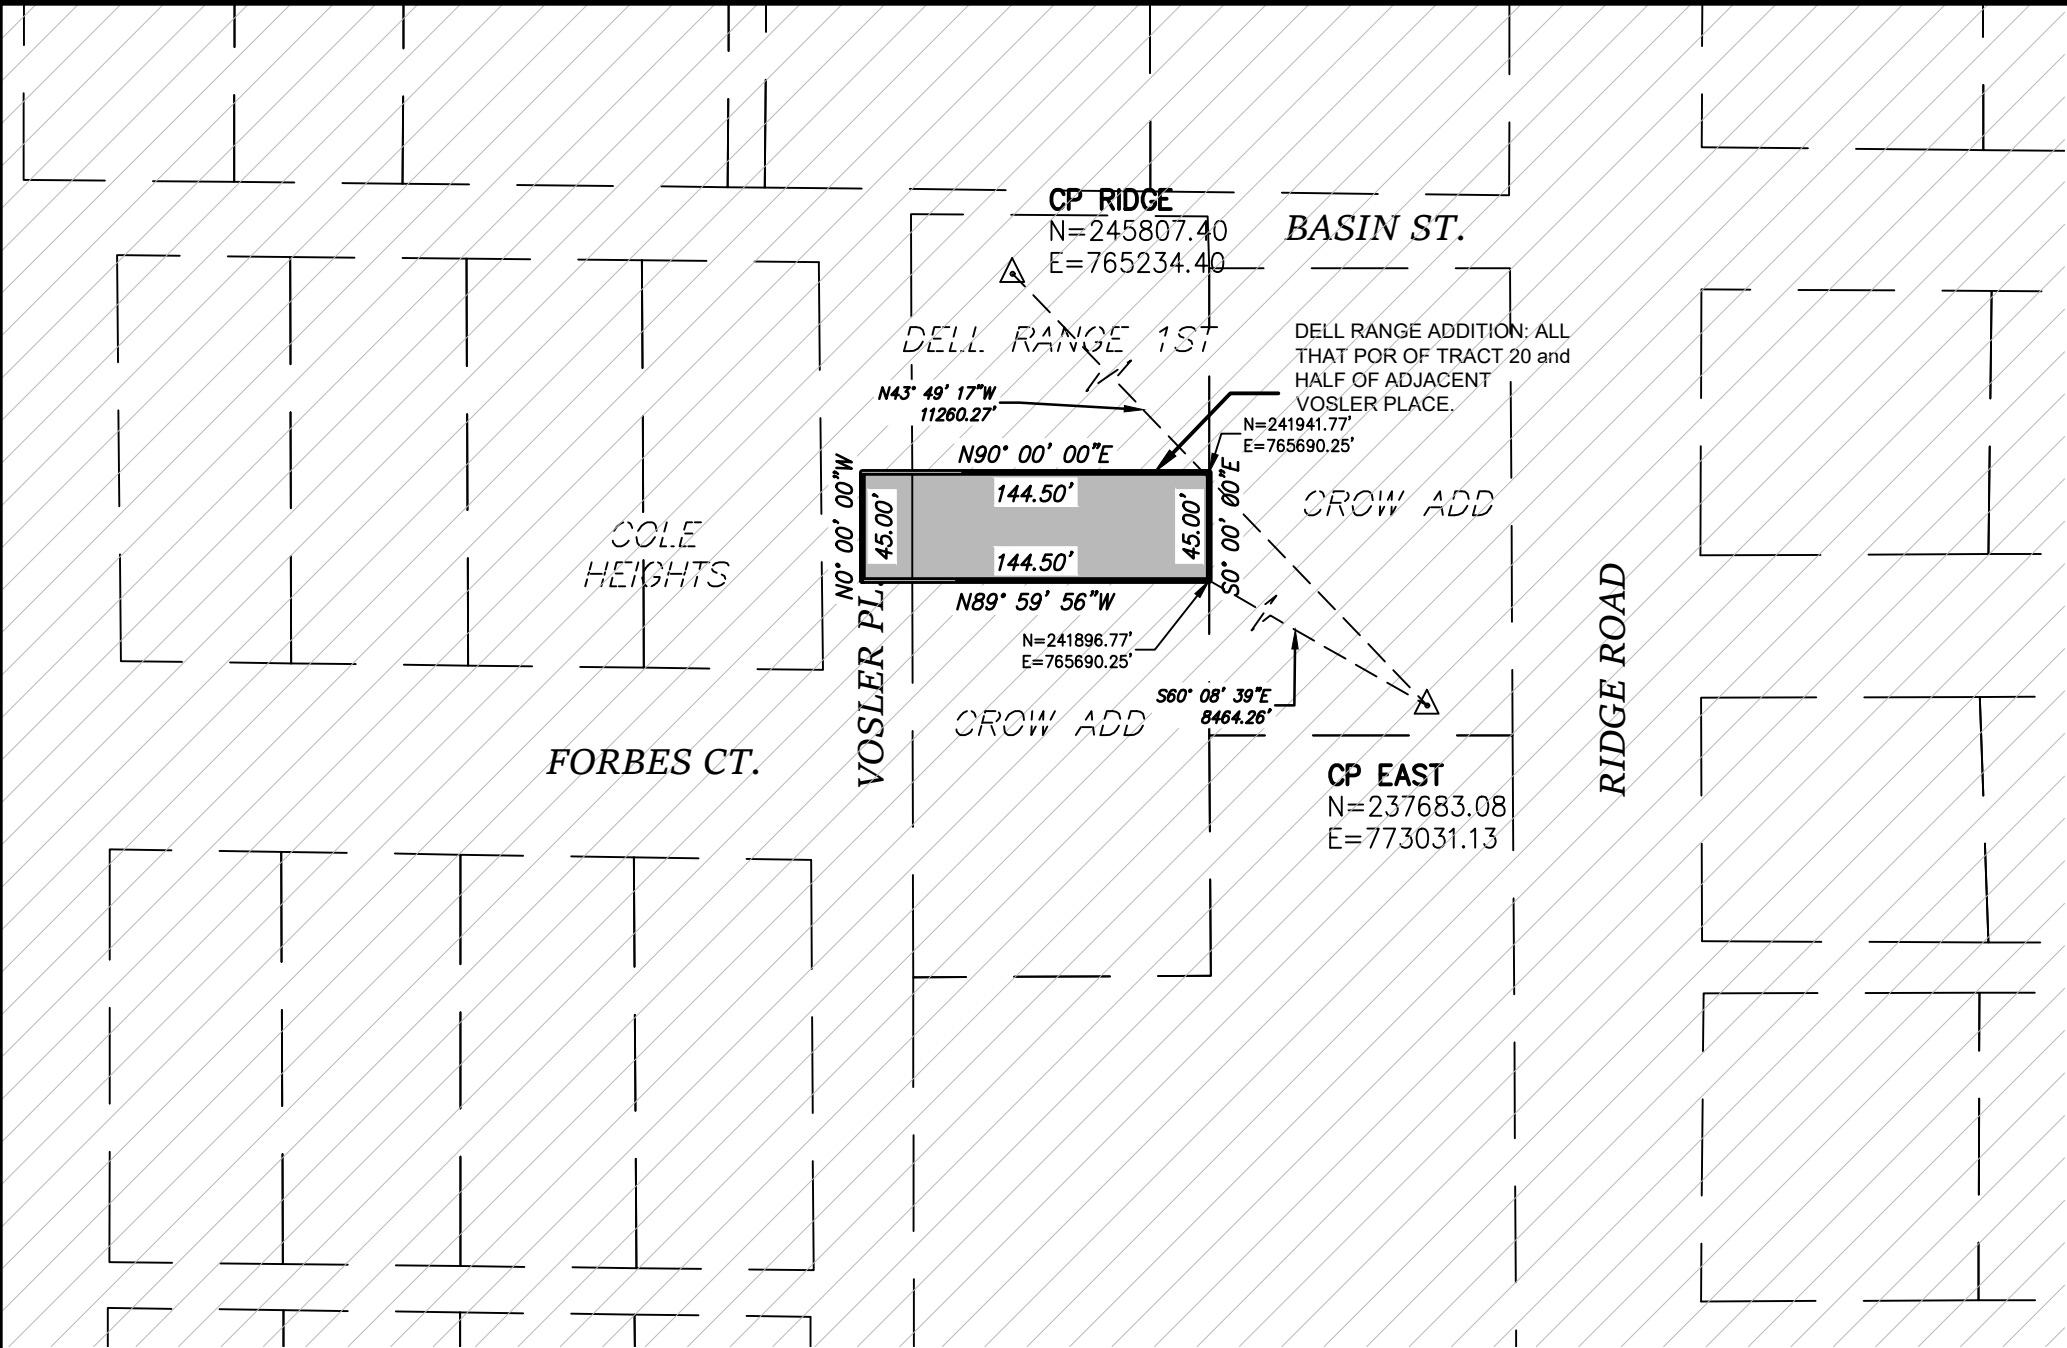

LEGEND

-  AREA TO BE ANNEXED
-  EXISTING CITY LIMITS

ANNEXATION AREA

TOTAL AREA: 0.15 ACRES
ABUTTING ANNEXATION AND RATIO TO TOTAL PERIMETER - 100%

APPROVALS

Approved by the City Council of the City of Cheyenne, Wyoming,
this _____ day of _____, 2025.

Mayor

ATTEST: _____
City Clerk

FILING RECORD




CERTIFICATE OF SURVEYOR

I, JEFFREY B. JONES, A PROFESSIONAL LAND SURVEYOR IN THE STATE OF WYOMING, HEREBY STATE THAT THESE ANNEXATION MAPS WERE PREPARED FROM OFFICIAL PLATS AND DEEDS OF RECORD AND FROM NOTES OF A SURVEY CONDUCTED BY MYSELF OR UNDER MY DIRECT SUPERVISION DURING THE MONTHS OF FEBRUARY –JUNE, 2025, AND THAT THIS MAP CORRECTLY REPRESENTS SAID SURVEY OF THE LAND DEPICTED HEREON TO THE BEST OF MY KNOWLEDGE.

ANNEXATION DESCRIPTION - G

LOT 5, COLE HEIGHTS ADDITION and THE ADJACENT 60' RIGHT OF WAY OF COLE PLACE, CITY OF CHEYENNE, LARAMIE COUNTY, WYOMING.

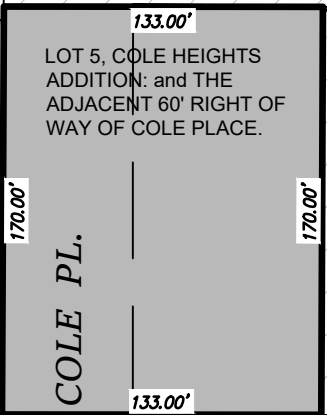

N=241783.58'
E=765311.54'

CP RIDGE
N=245807.40
E=765234.40

N43° 49' 17"W
11260.27'

N=241613.58'
E=765310.57'

S63° 01' 10"E
8663.48'

CP EAST
N=237683.08
E=773031.13

LEGEND



AREA TO BE ANNEXED



EXISTING CITY LIMITS

ANNEXATION AREA

TOTAL AREA: 0.50 ACRES

ABUTTING ANNEXATION AND RATIO TO TOTAL PERIMETER - 100%

APPROVALS

Approved by the City Council of the City of Cheyenne, Wyoming,
this _____ day of _____, 2025.


Mayor

ATTEST:

City Clerk

FILING RECORD

BASIS OF BEARINGS:
WYOMING STATE PLANE COORDINATES,
EAST ZONE, NAD83–2011,
US SURVEY FEET, DISTANCES ARE GRID
DISTANCES.

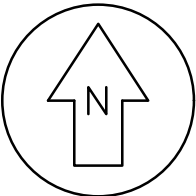

0 80'

Scale: 1"=80'

CERTIFICATE
OF
SURVEYOR


SHEET #
8 OF 9

I, JEFFREY B. JONES, A PROFESSIONAL LAND SURVEYOR IN THE STATE OF WYOMING, HEREBY STATE THAT THESE ANNEXATION MAPS WERE PREPARED FROM OFFICIAL PLATS AND DEEDS OF RECORD AND FROM NOTES OF A SURVEY CONDUCTED BY MYSELF OR UNDER MY DIRECT SUPERVISION DURING THE MONTHS OF FEBRUARY –JUNE, 2025, AND THAT THIS MAP CORRECTLY REPRESENTS SAID SURVEY OF THE LAND DEPICTED HEREON TO THE BEST OF MY KNOWLEDGE.

COUNTY POCKETS
FORCED ANNEXATION
NUMBER 5 – EXHIBIT H

REVISED: 5/1/2025
25112 EXHIBIT H.DWG

STEEL SURVEYING SERVICES, LLC
PROFESSIONAL LAND SURVEYORS
PLANNING & DEVELOPMENT SPECIALISTS
1108 WEST 19th ST. CHEYENNE, WY. 82001 • (307) 634-7223
256 GILCHRIST ST. WHEATLAND, WY. 82201 • (307) 582-9789
www.SteelSurvey.com • info@SteelSurvey.com

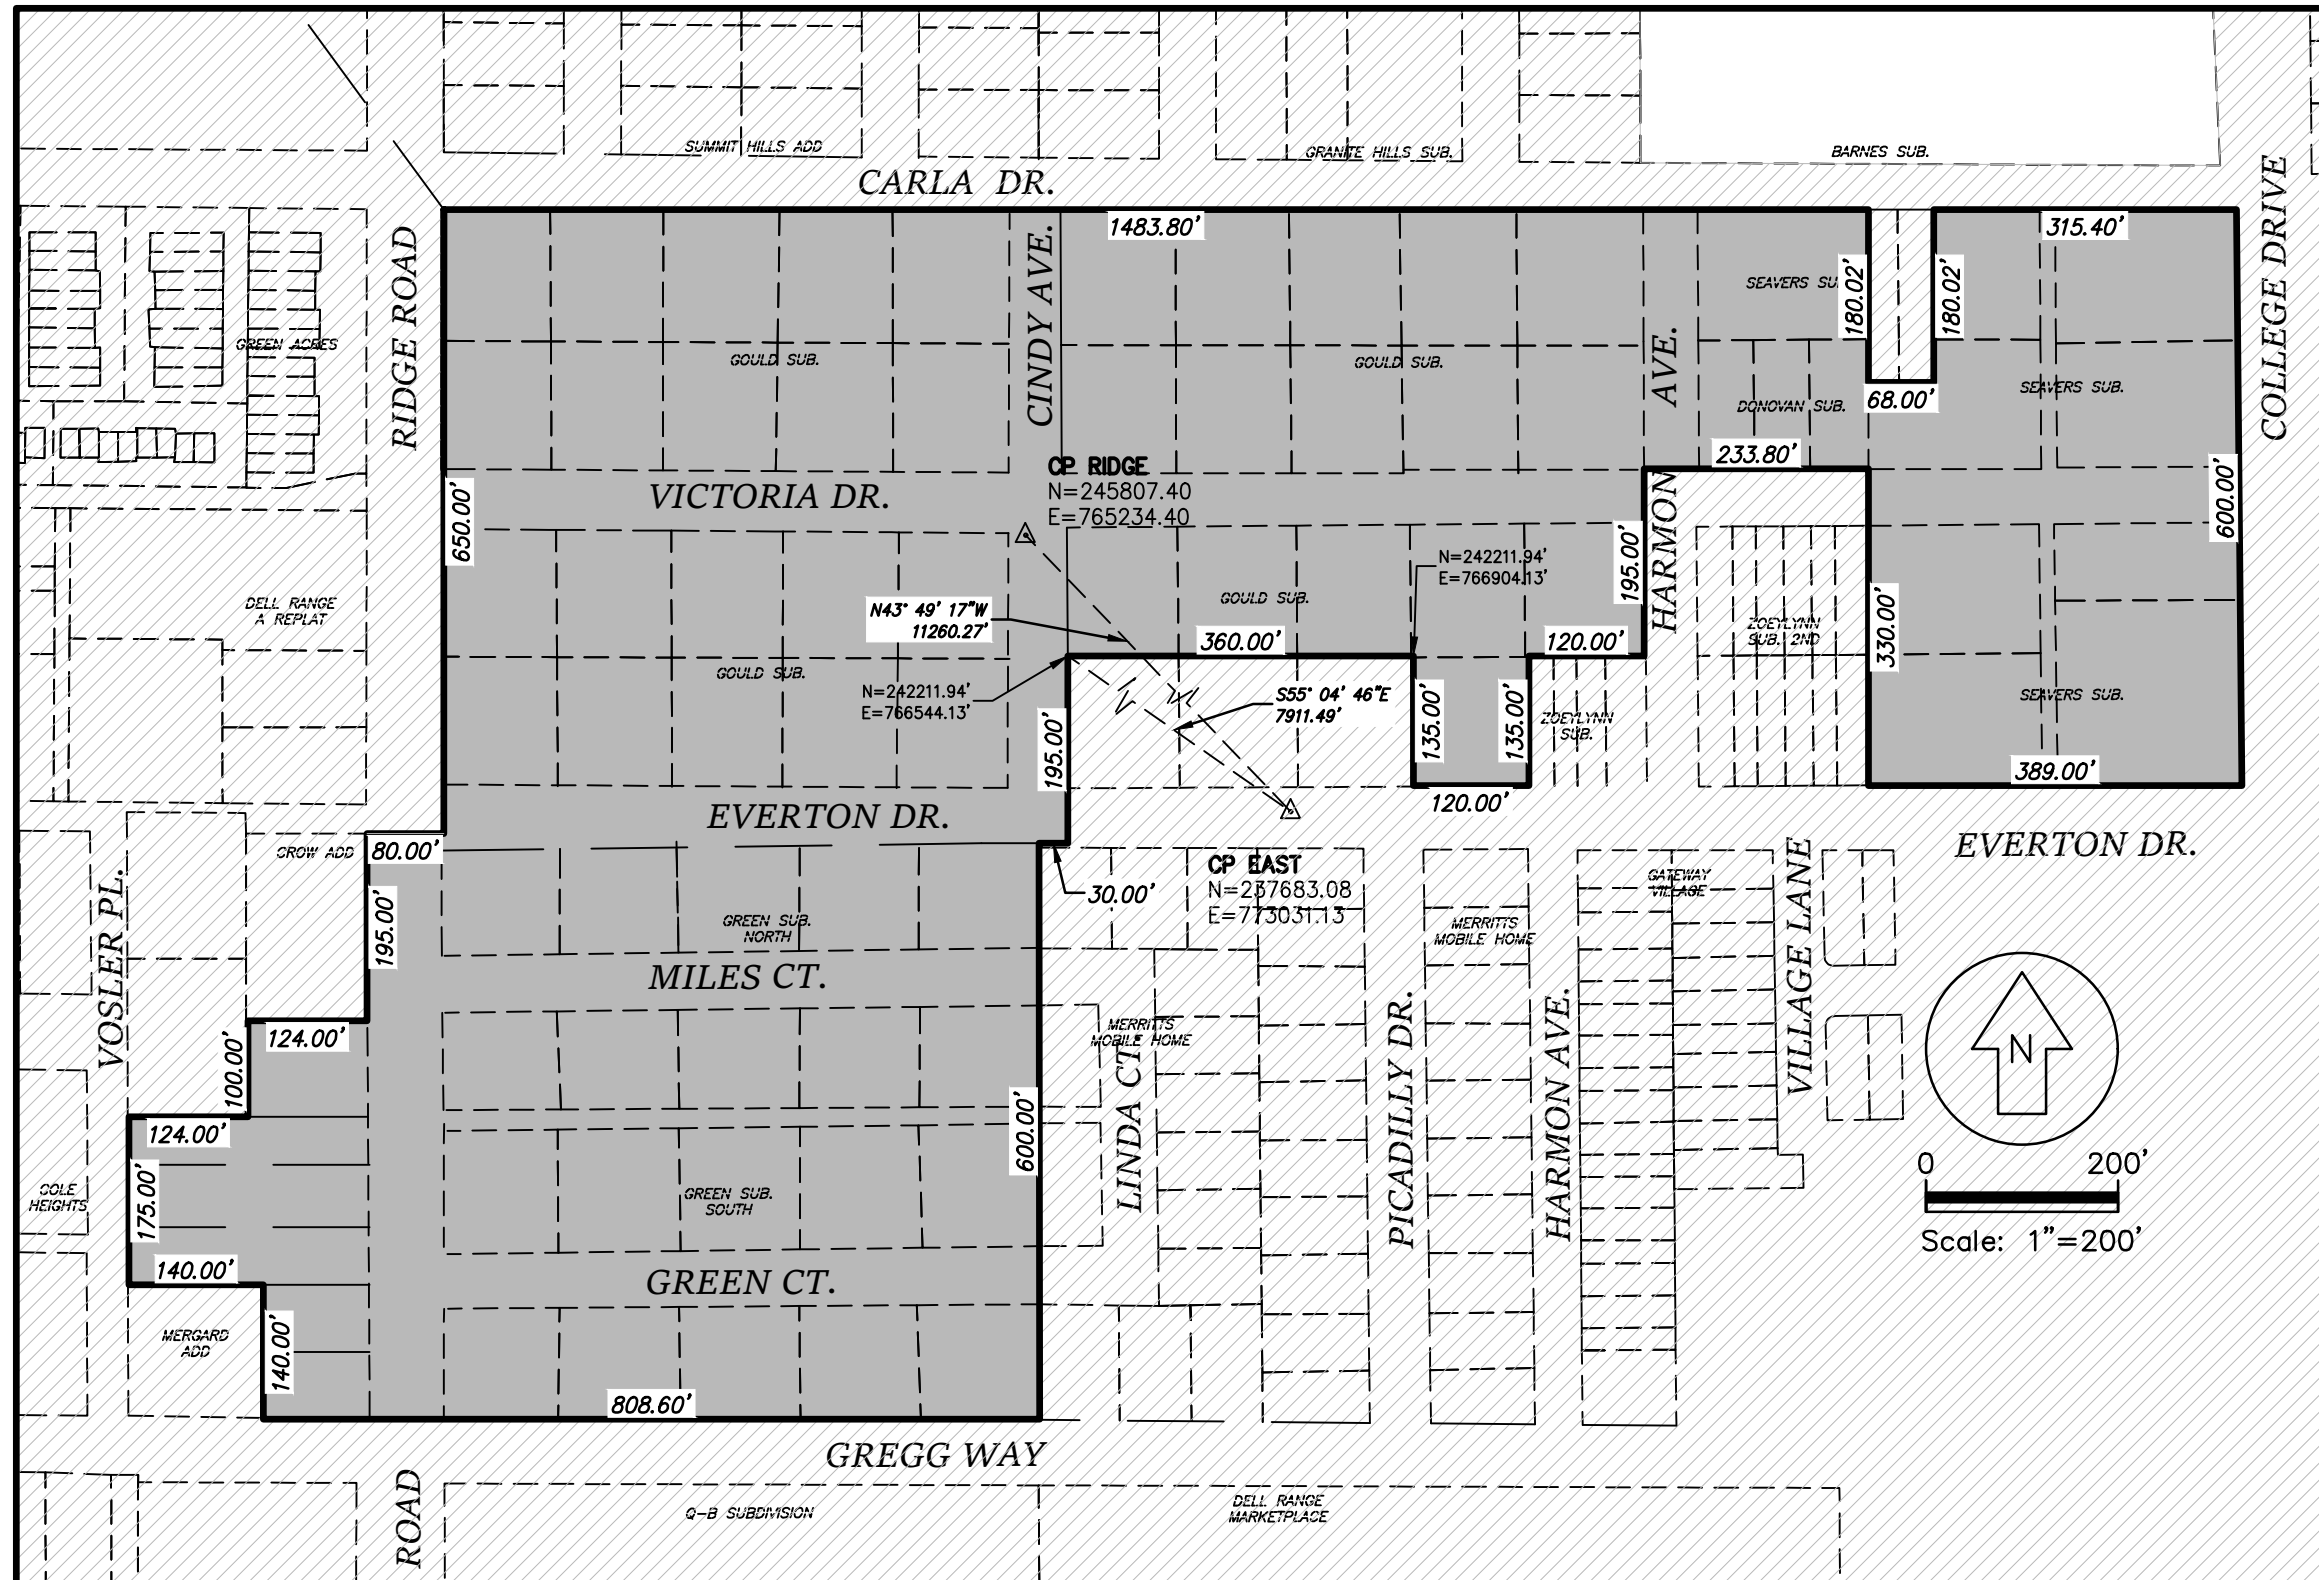

BASIS OF BEARINGS:
WYOMING STATE PLANE COORDINATES,
EAST ZONE, NAD83–2011,
US SURVEY FEET, DISTANCES ARE GRID
DISTANCES.

LEGEND

AREA TO BE ANNEXED

EXISTING CITY LIMITS

FILING RECORD

ANNEXATION AREA

TOTAL AREA: 34.17 ACRES

ABUTTING ANNEXATION AND RATIO TO TOTAL
PERIMETER - 100%

APPROVALS

Approved by the City Council of the City of Cheyenne, Wyoming,
this _____ day of _____, 2025.

Mayor

ATTEST:

City Clerk

Pidn: AS OF 4-7-25	Pidn: AS OF 4-7-25	Pidn: AS OF 4-7-25	Pidn: AS OF 4-7-25	Pidn: AS OF 4-7-25	Pidn: AS OF 4-7-25	Pidn: AS OF 4-7-25	Pidn: AS OF 4-7-25
14662111905000	14662231200500	14662111905000	14662231001200	14662231400500	14662231800700	14662233700100	14662232700900
14662231000400	14662231200400	14662231000400	14662231500300	14662231401300	14662231800600	14662232001000	14662232700700
14662231000300	14662231201900	14662231000300	14662231500900	14662231401200	14662231800500	14662232001100	14662232700400
14662231000200	14662231200100	14662231000200	14662231501000	14662231400300	14662232000200	14662232001200	14662232700600
14662231001000	14662231200900	14662231001000	14662231500400	14662231400200	14662232000300	14662231802800	14662232700500
14662231000900	14662231201100	14662231000900	14662231500500	14662231400100	14662232000400	14662231802900	14662231300100
14662231100400	14662231201000	14662231100400	14662231500600	14662231400700	14662232000500	14662231803000	14662231300600
14662231100300	14662231201500	14662231100300	14662231500700	14662231400800	14662232000600	14662231803100	14662231300200
14662231100200	14662231201400	14662231100200	14662231501100	14662231800900	14662232000700	14662231803200	14662231300300
14662231100100	14662231201300	14662231100100	14662231500800	14662231800800	14662232001800	14662232701000	14048000200090

ANNEXATION DESCRIPTION - H

ALL PARCELS AND PLATTED RIGHTS OF WAY LOCATED WITHIN: BEGINNING AT THE SOUTHWEST CORNER OF LOT 5, BLOCK 4, GOULD SUBDIVISION, THENCE SOUTHERLY ALONG THE EASTERLY RIGHT OF WAY OF CINDY AVE. A DISTANCE OF 195.00 FEET TO A POINT ON THE SOUTHERLY RIGHT OF WAY OF EVERTON DR.; THENCE WESTERLY ALONG SAID RIGHT OF WAY 30.00 FEET TO THE NORTHEASTERLY CORNER OF TRACT 20 OF GREEN SUBDIVISION OF THE NORTH HALF OF TRACT 19, DELL RANGE ADDITION; THENCE SOUTHERLY A DISTANCE OF 600.00 FEET ALONG THE EASTERLY BOUNDARIES OF GREEN SUBDIVISIONS OF BOTH THE NORTH HALF AND SOUTH HALF OF TRACT 19, DELL RANGE ADDITION TO A POINT ON THE NORTHERLY RIGHT OF WAY OF GREGG WAY; THENCE WESTERLY ALONG SAID RIGHT OF WAY A DISTANCE OF 700.60 FEET TO THE SOUTHEASTERLY CORNER OF TRACT 20, DELL RANGE ADDITION; THENCE INCLUSIVE OF EXISTING PARCELS BEING PORTIONS OF TRACT 20, DELL RANGE ADDITION DESCRIBED AS CONTINUING WESTERLY ALONG SAID RIGHT OF WAY A DISTANCE OF 108 FEET TO A POINT; THENCE NORTHERLY 140.00 FEET TO A POINT; THENCE WESTERLY 140.00 FEET TO A POINT ON THE EASTERLY RIGHT OF WAY OF VOSLER PLACE; THENCE NORTHERLY ALONG SAID RIGHT OF WAY 175.00 FEET TO THE SOUTHWESTERLY CORNER OF LOT 1, BLOCK 1, CROW ADDITION; THENCE ALONG THE BOUNDARY OF SAID CROW ADDITION THE FOLLOWING FOUR COURSES; THENCE EASTERLY A DISTANCE OF 124.00 FEET TO A POINT; THENCE NORTHERLY 100 FEET TO A POINT; THENCE EASTERLY 124.00 FEET TO A POINT ON THE WESTERLY RIGHT OF WAY OF RIDGE ROAD; THENCE NORTHERLY ALONG SAID RIGHT OF WAY A DISTANCE OF 195.00 FEET TO THE POINT OF INTERSECTION WITH THE SOUTHERLY RIGHT OF WAY OF BASIN STREET EXTENDED; THENCE EASTERLY 80.00 FEET TO A POINT ON THE EASTERLY RIGHT OF WAY OF RIDGE ROAD; THENCE NORTHERLY ALONG SAID RIGHT OF WAY, BEING THE WESTERLY BOUNDARY OF GOULD SUBDIVISION, A DISTANCE OF 650 FEET TO THE NORTHWESTERLY CORNER OF LOT 5, BLOCK 2, GOULD SUBDIVISION; THENCE EASTERLY ALONG THE SOUTHERLY RIGHT OF WAY OF CARLA DRIVE A DISTANCE OF 1483.80 FEET TO THE NORTHEASTERLY CORNER OF LOT 5, BLOCK 1, SEAVER SUBDIVISION; THENCE THE FOLLOWING THREE COURSES ALONG THE BOUNDARIES OF SEILOFF ADDITION, THENCE SOUTHERLY 180.02 FEET; THENCE EASTERLY 68.00 FEET; THENCE NORTHERLY 180.02 FEET TO THE SOUTHERLY RIGHT OF WAY OF CARLA DRIVE; THENCE CONTINUING EASTERLY ALONG SAID SOUTHERLY RIGHT OF WAY A DISTANCE OF 315.40 FEET TO THE NORTHEASTERLY CORNER OF LOT 1, BLOCK 1, SEAVERS SUBDIVISION; THENCE SOUTHERLY ALONG THE WESTERLY RIGHT OF WAY OF COLLEGE DRIVE A DISTANCE OF 600.00 FEET TO THE SOUTHEASTERLY CORNER OF LOT 2, BLOCK 2, SEAVERS SUBDIVISION; THENCE WESTERLY 389.00 FEET ALONG THE NORTHERLY RIGHT OF WAY OF EVERTON DRIVE TO THE SOUTHWESTERLY CORNER OF LOT 3, BLOCK 2, SEAVERS SUBDIVISION; THENCE NORTHERLY 330.00 FEET TO THE SOUTHEASTERLY CORNER OF DONOVAN SUBDIVISION; THENCE WESTERLY A DISTANCE OF 233.80 FEET ALONG THE NORTHERLY RIGHT OF WAY OF VICTORIA DRIVE TO THE SOUTHEASTERLY CORNER OF LOT 2, BLOCK 1, GOULD SUBDIVISION 2ND FILING; THENCE SOUTHERLY A DISTANCE OF 195.00 FEET TO THE SOUTHEASTERLY CORNER OF LOT 1, BLOCK 4, GOULD SUBDIVISION; THENCE WESTERLY A DISTANCE OF 120.00 FEET TO THE SOUTHWESTERLY CORNER OF SAID LOT 1, BLOCK 4, GOULD SUBDIVISION; THENCE SOUTHERLY A DISTANCE OF 135.00 FEET TO THE SOUTHEASTERLY CORNER OF LOT 9, BLOCK 4, GOULD SUBDIVISION; THENCE WESTERLY A DISTANCE OF 120.00 FEET ALONG THE NORTHERLY RIGHT OF WAY OF EVERTON DRIVE TO THE SOUTHWESTERLY CORNER OF SAID LOT 9; THENCE NORTHERLY A DISTANCE OF 135.00 FEET TO THE NORTHWESTERLY CORNER OF SAID LOT 9; THENCE WESTERLY A DISTANCE OF 360.00 FEET TO THE POINT OF BEGINNING.

FILING RECORD

COUNTY POCKETS
FORCED ANNEXATION
NUMBER 5 – EXHIBIT H

REVISED: 4/11/2025
25112 EXHIBIT H.DWG

STIEL SURVEYING SERVICES, LLC
PROFESSIONAL LAND SURVEYORS
PLANNING & DEVELOPMENT SPECIALISTS
1108 WEST 10th ST. CHEYENNE, WY. 82001 • (307) 634-7223
256 GILCHRIST ST. WHEATLAND, WY. 82001 • (307) 582-3739
www.StielSurvey.com • info@StielSurvey.com

